



Обмерочный план квартиры

A

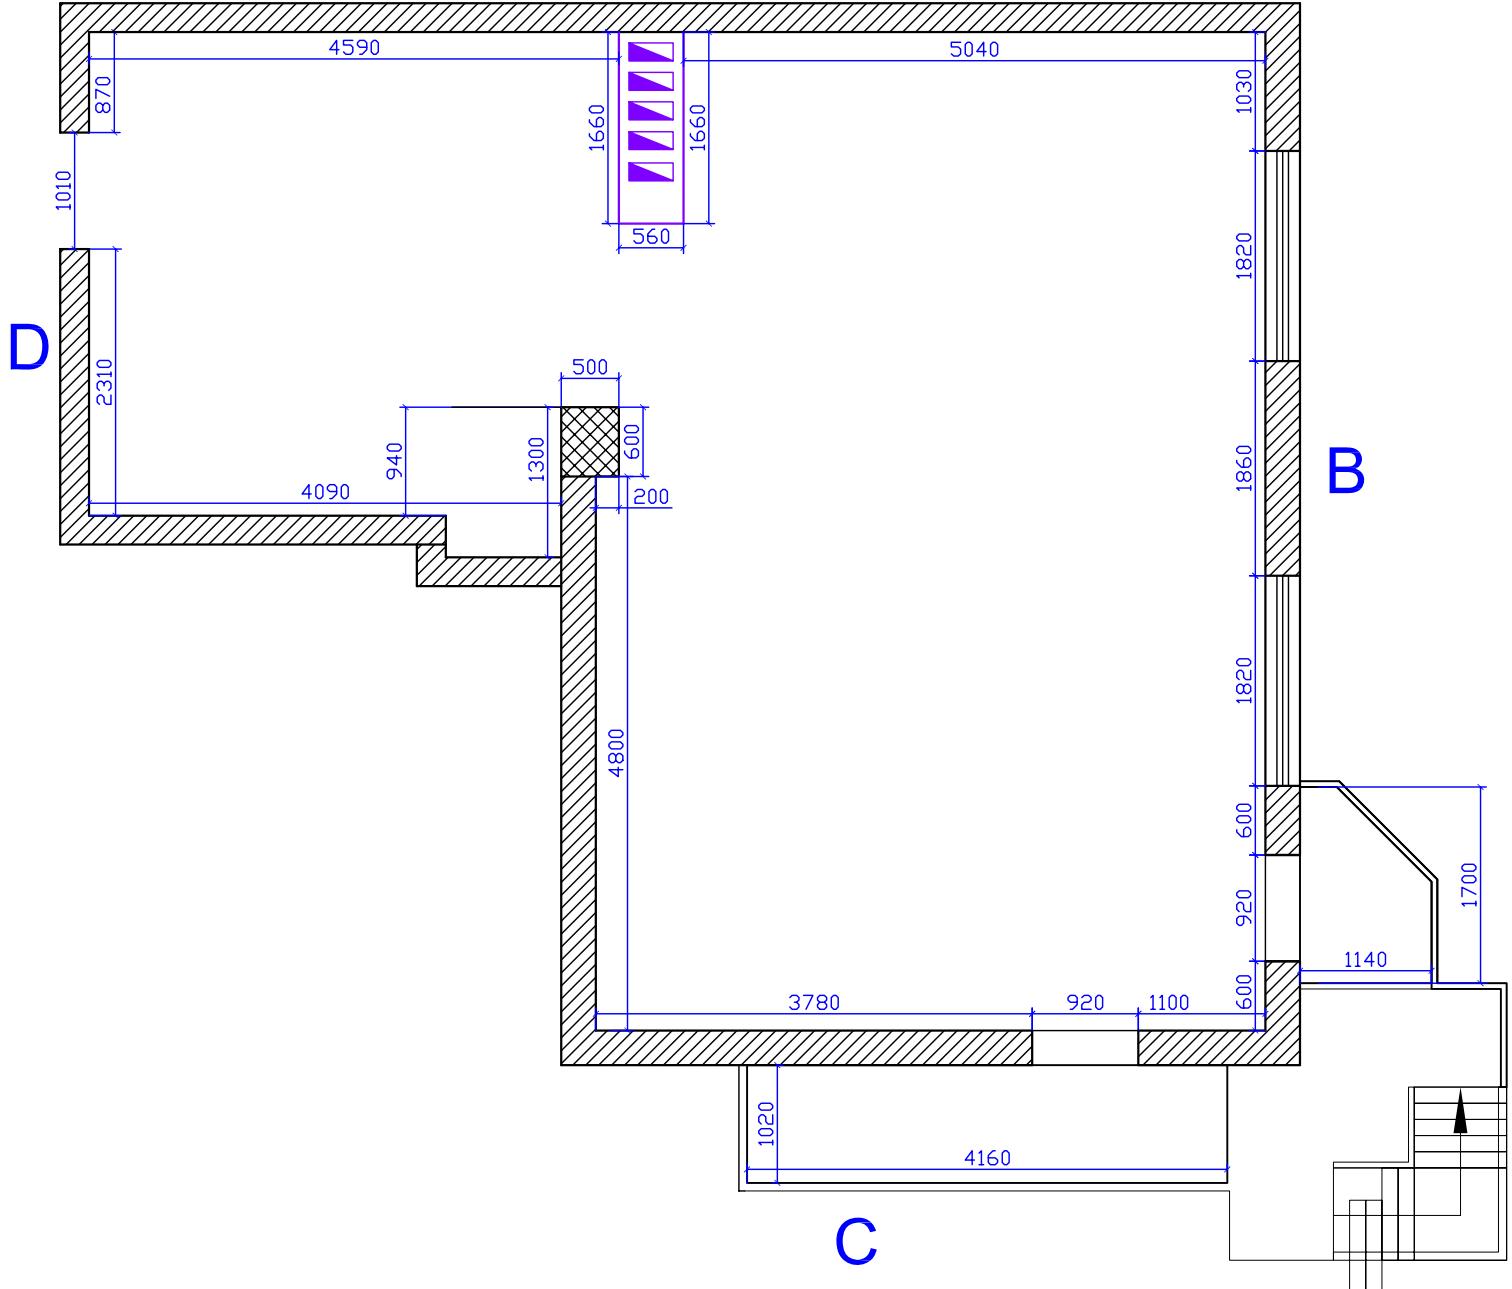


План возведения перегородок

A

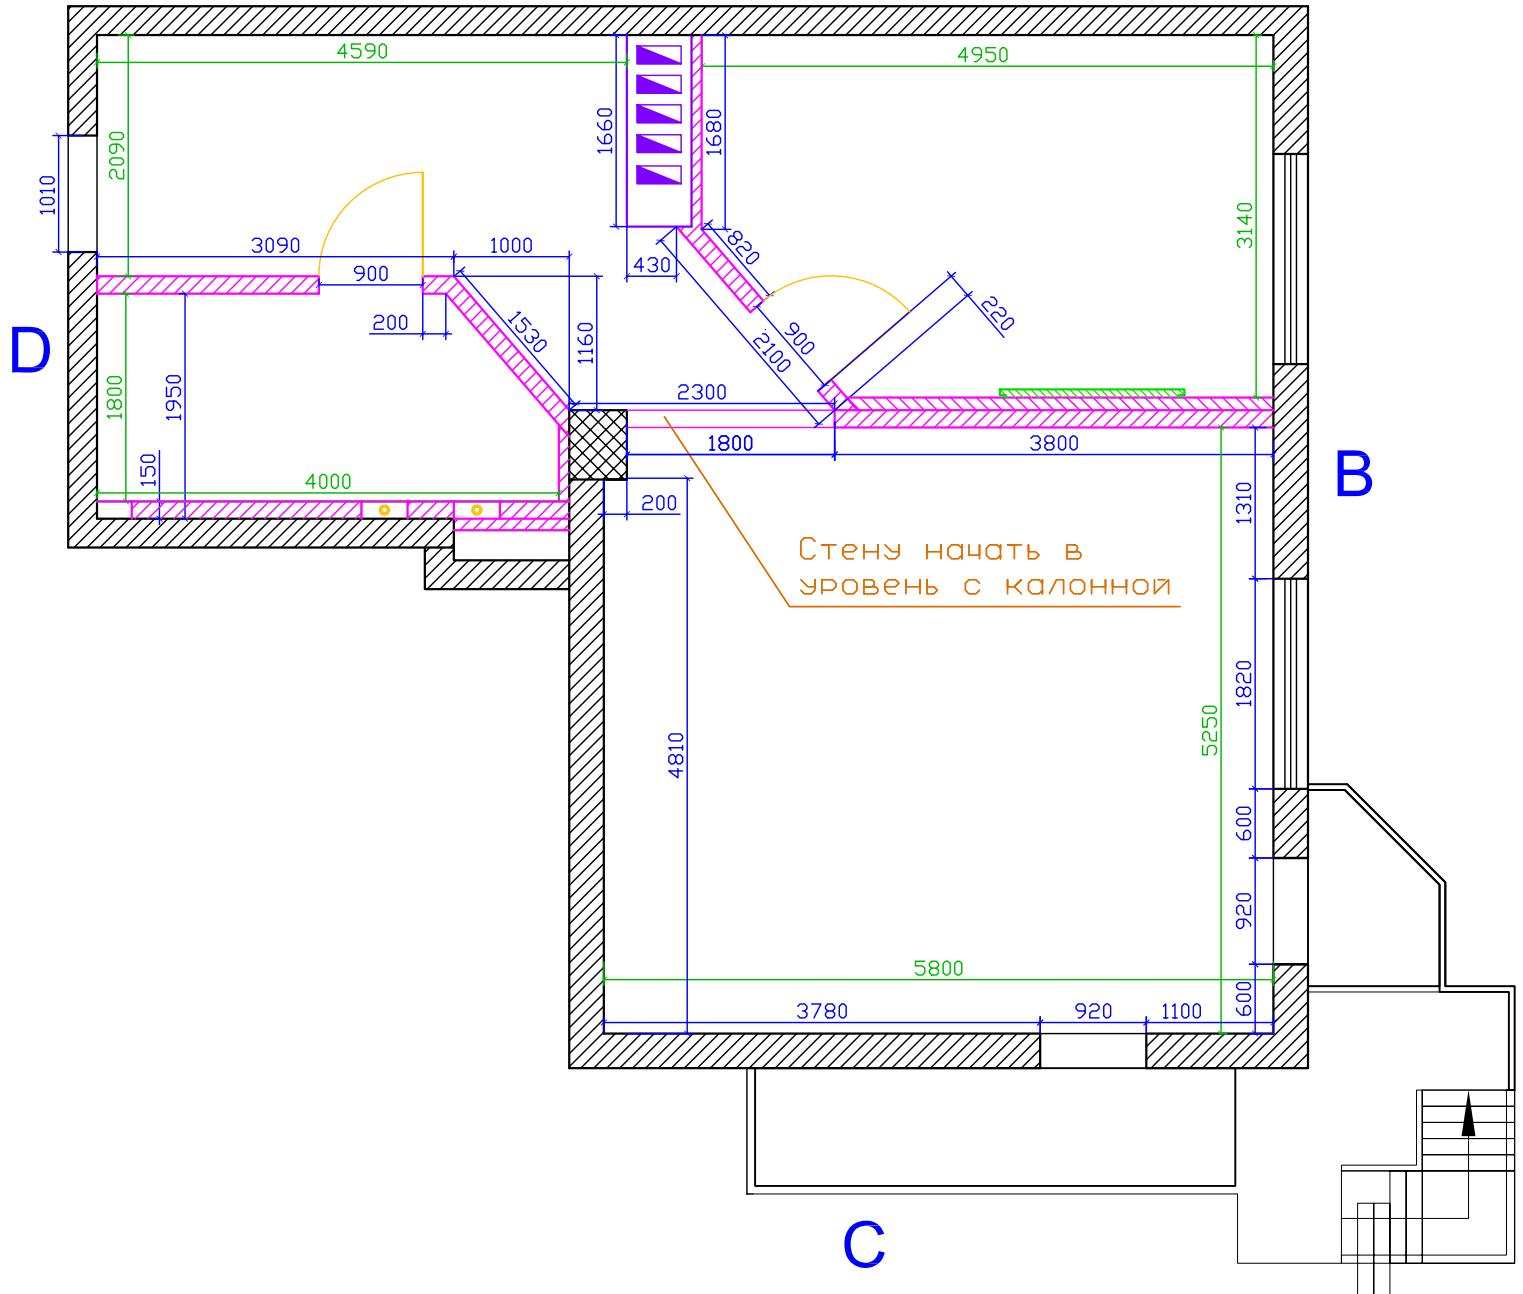

План расстановки мебели


A

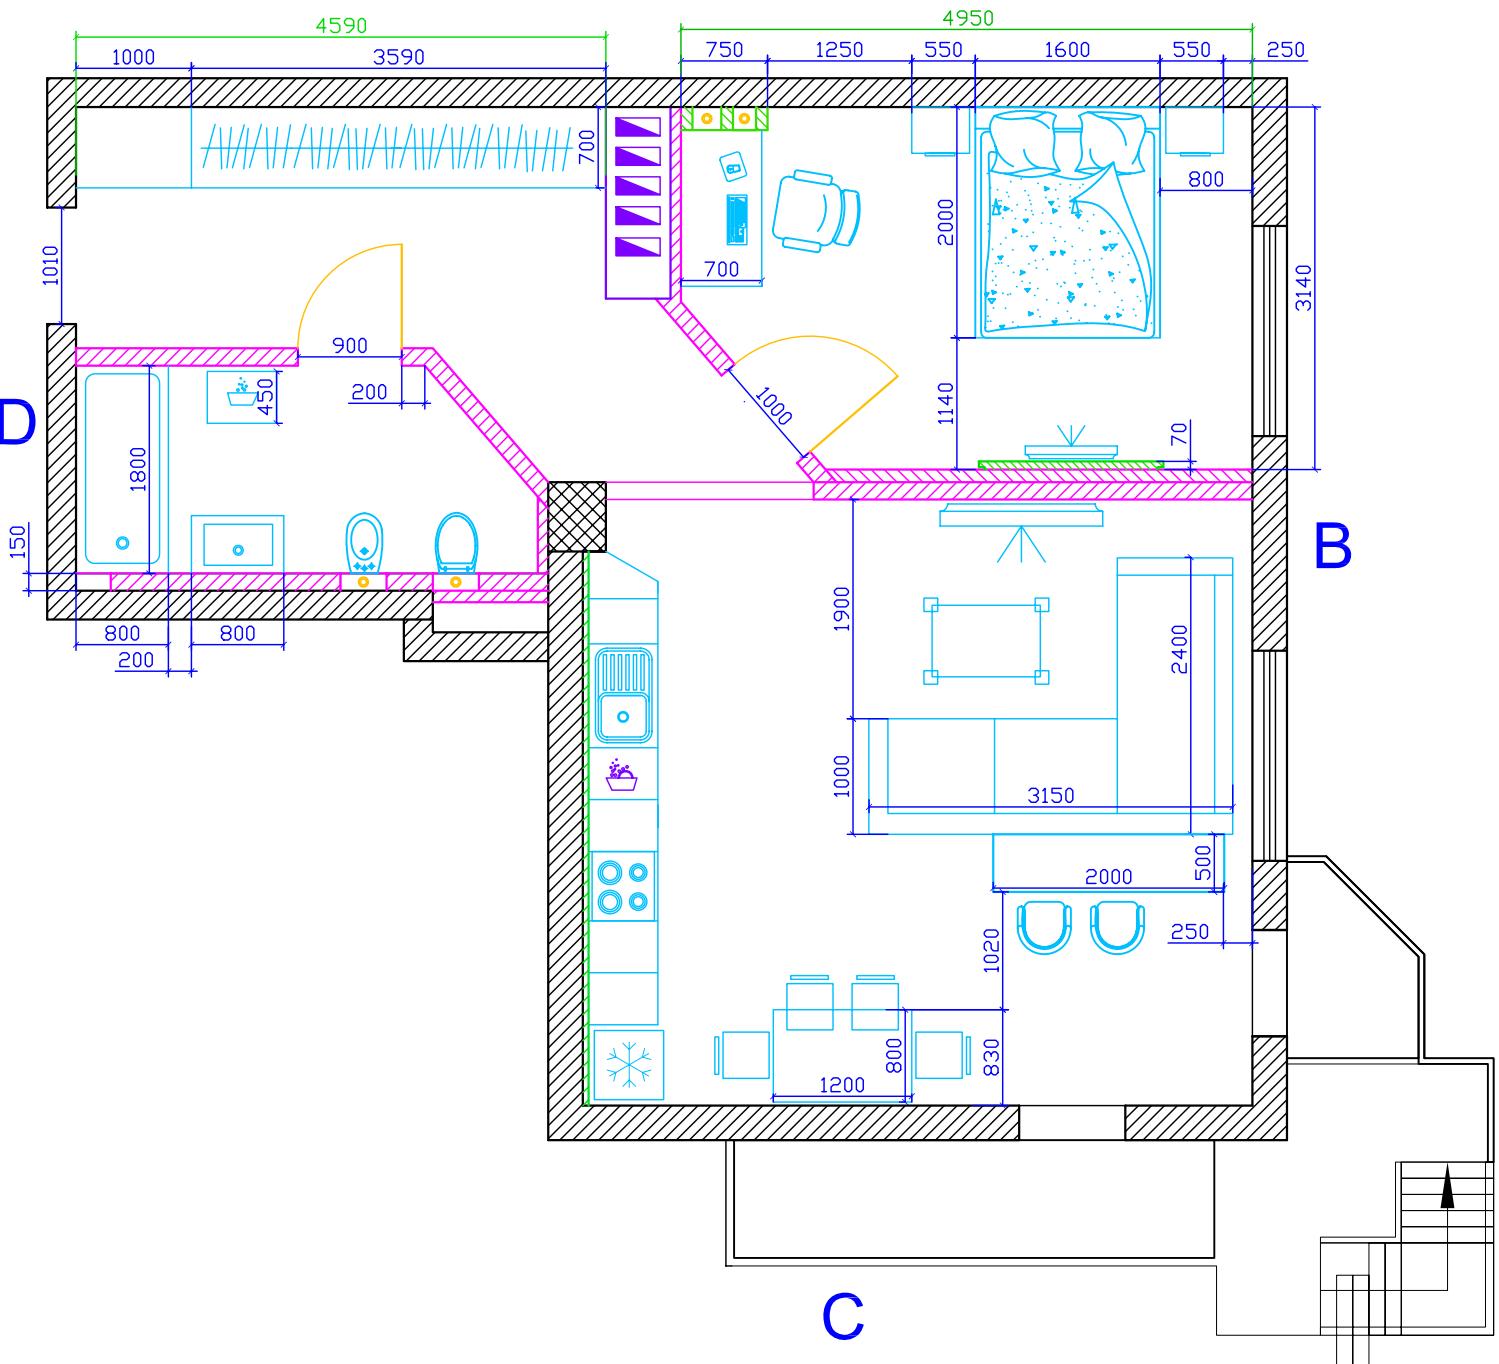

C

План полов

A

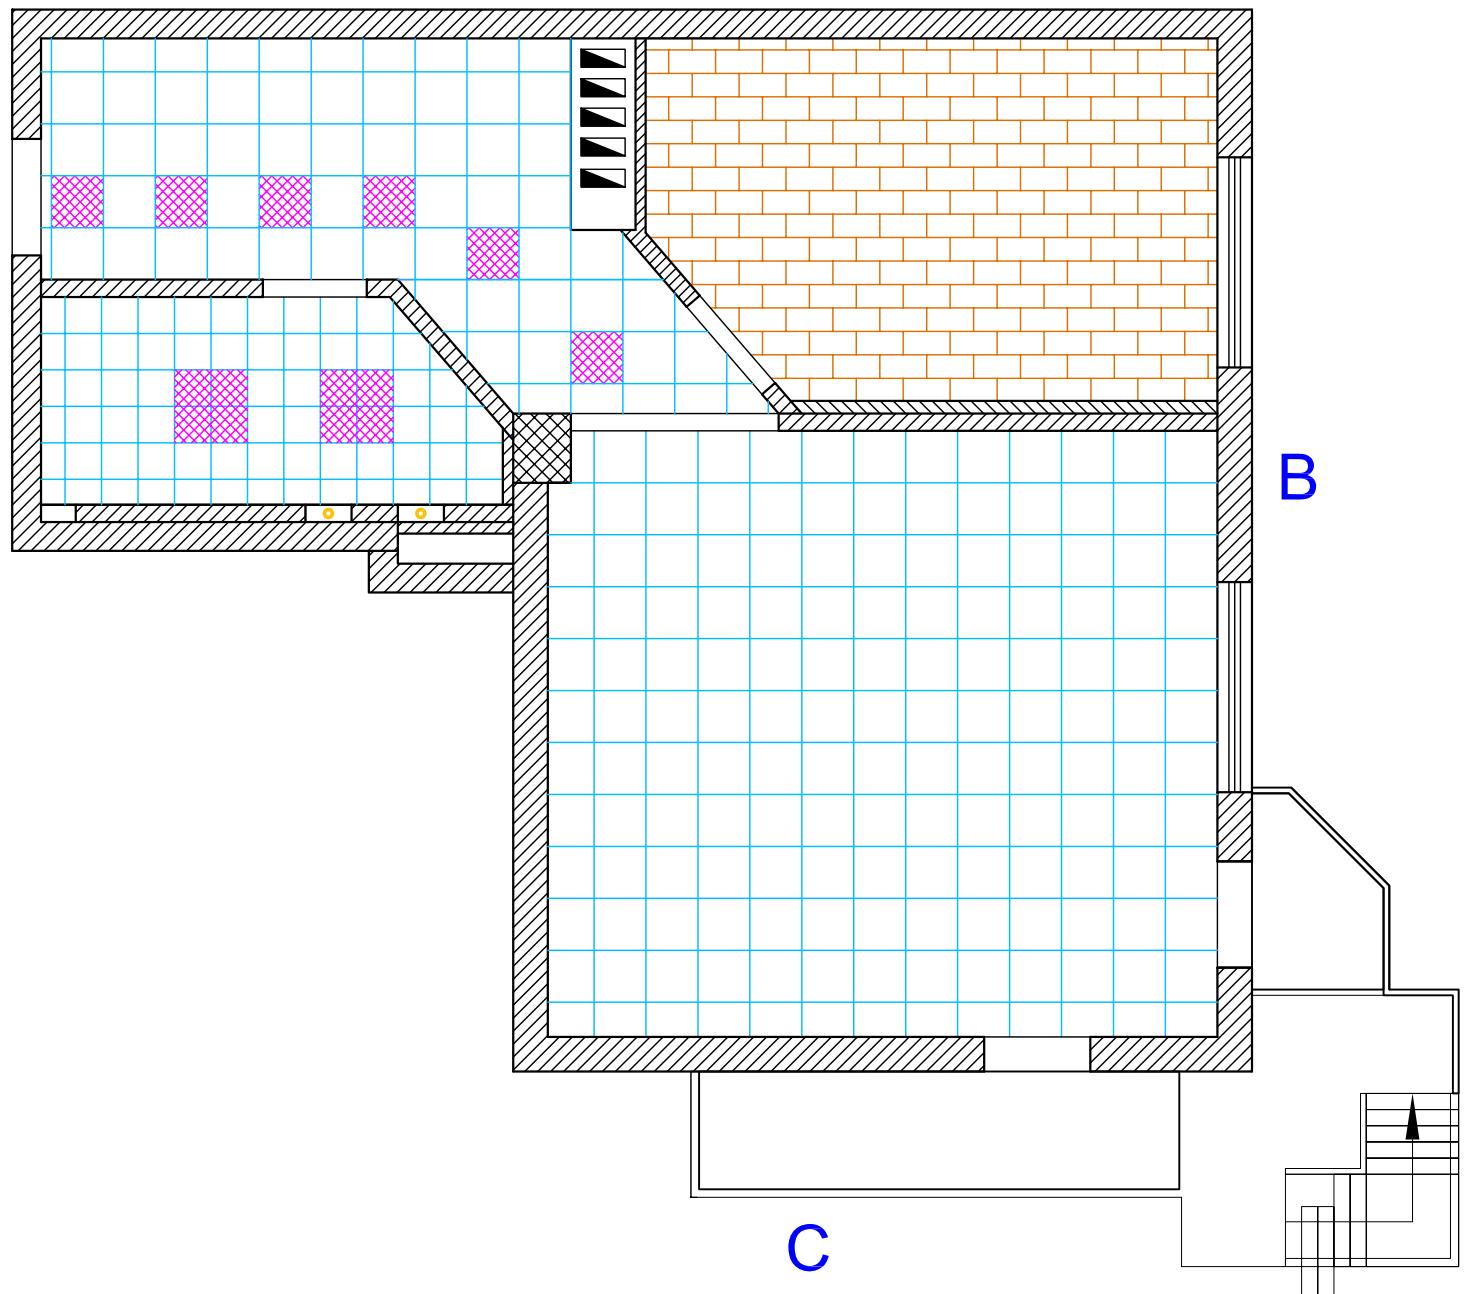

Коридор - 45x45 = 6шт Бежевая

Коридор - 45x45 = 65шт Коричневая

Гостиная - 45x45 = 156шт Бежевая


Спальня - 15,5м²

Ванная - 316x316 = 67шт Синяя

Ванная - 316x316 = 8шт Белая


План потолков

A

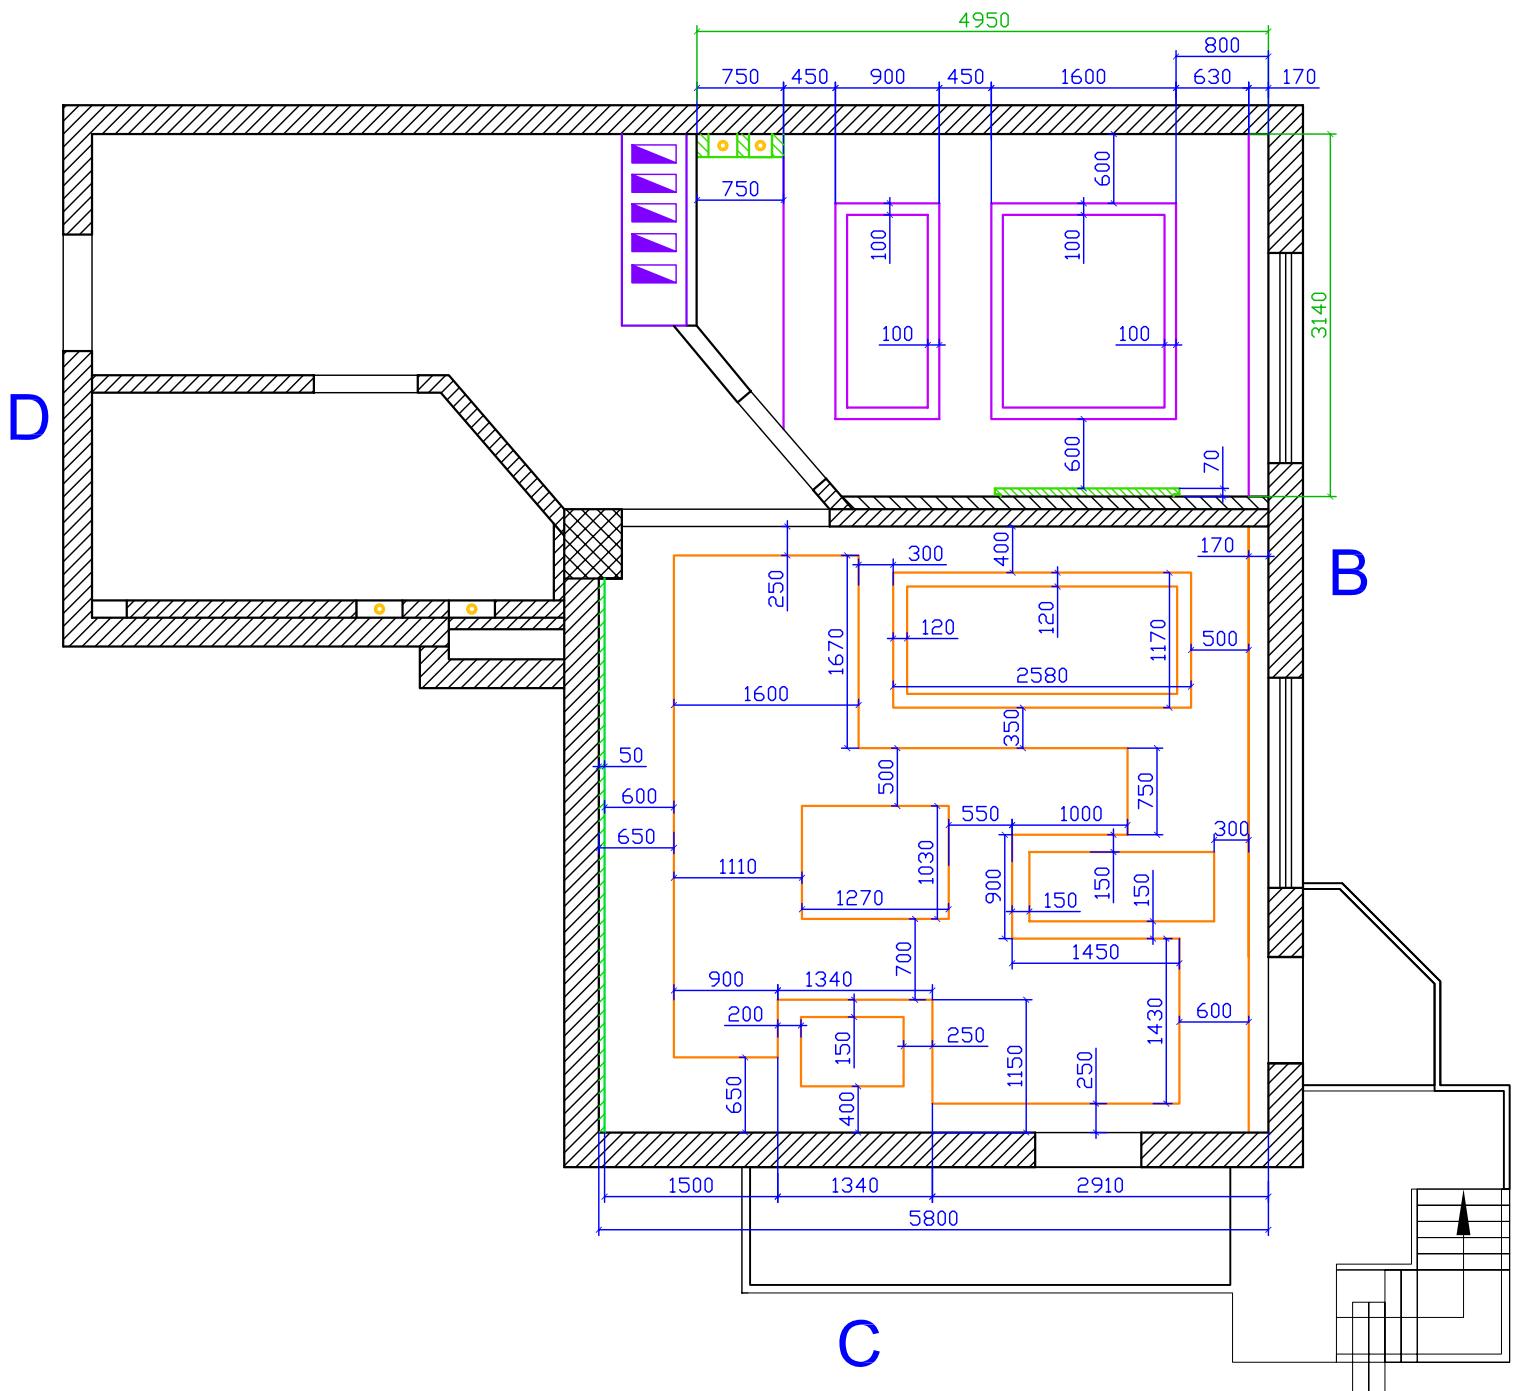

План уровней потолков

A

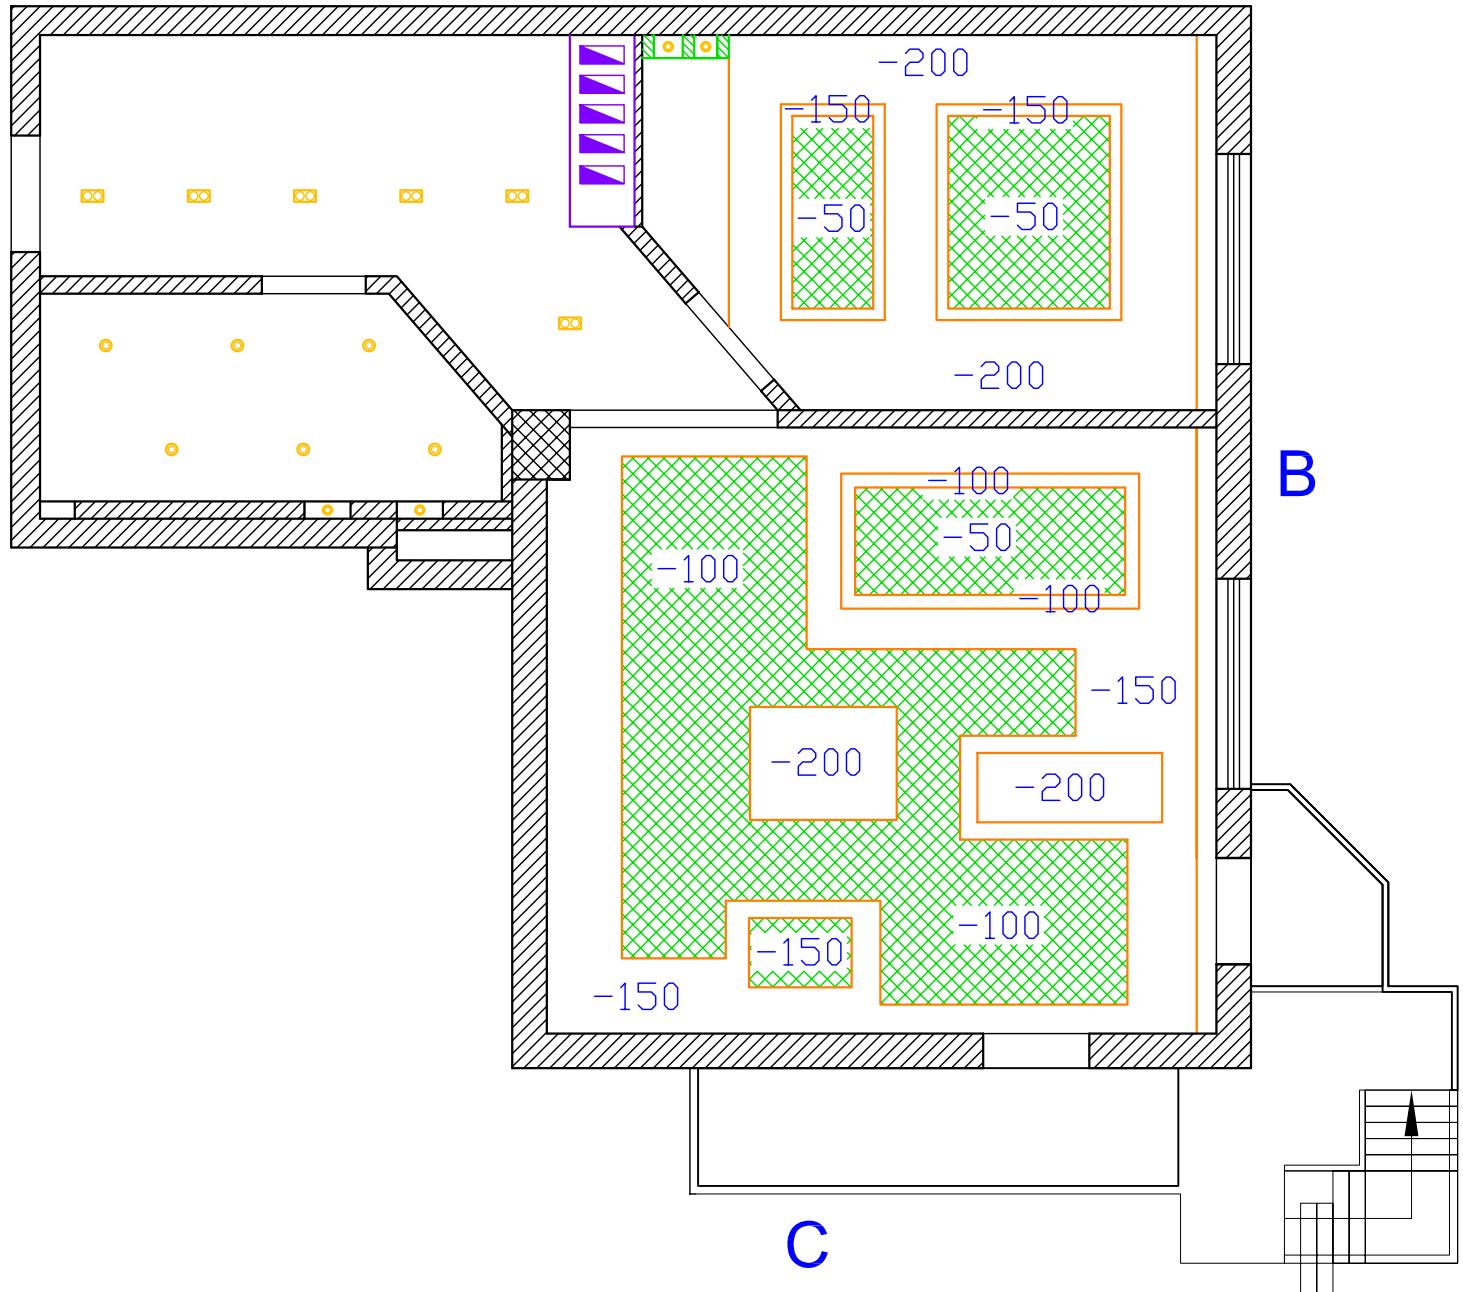


B

C

План расстановки светильников

A

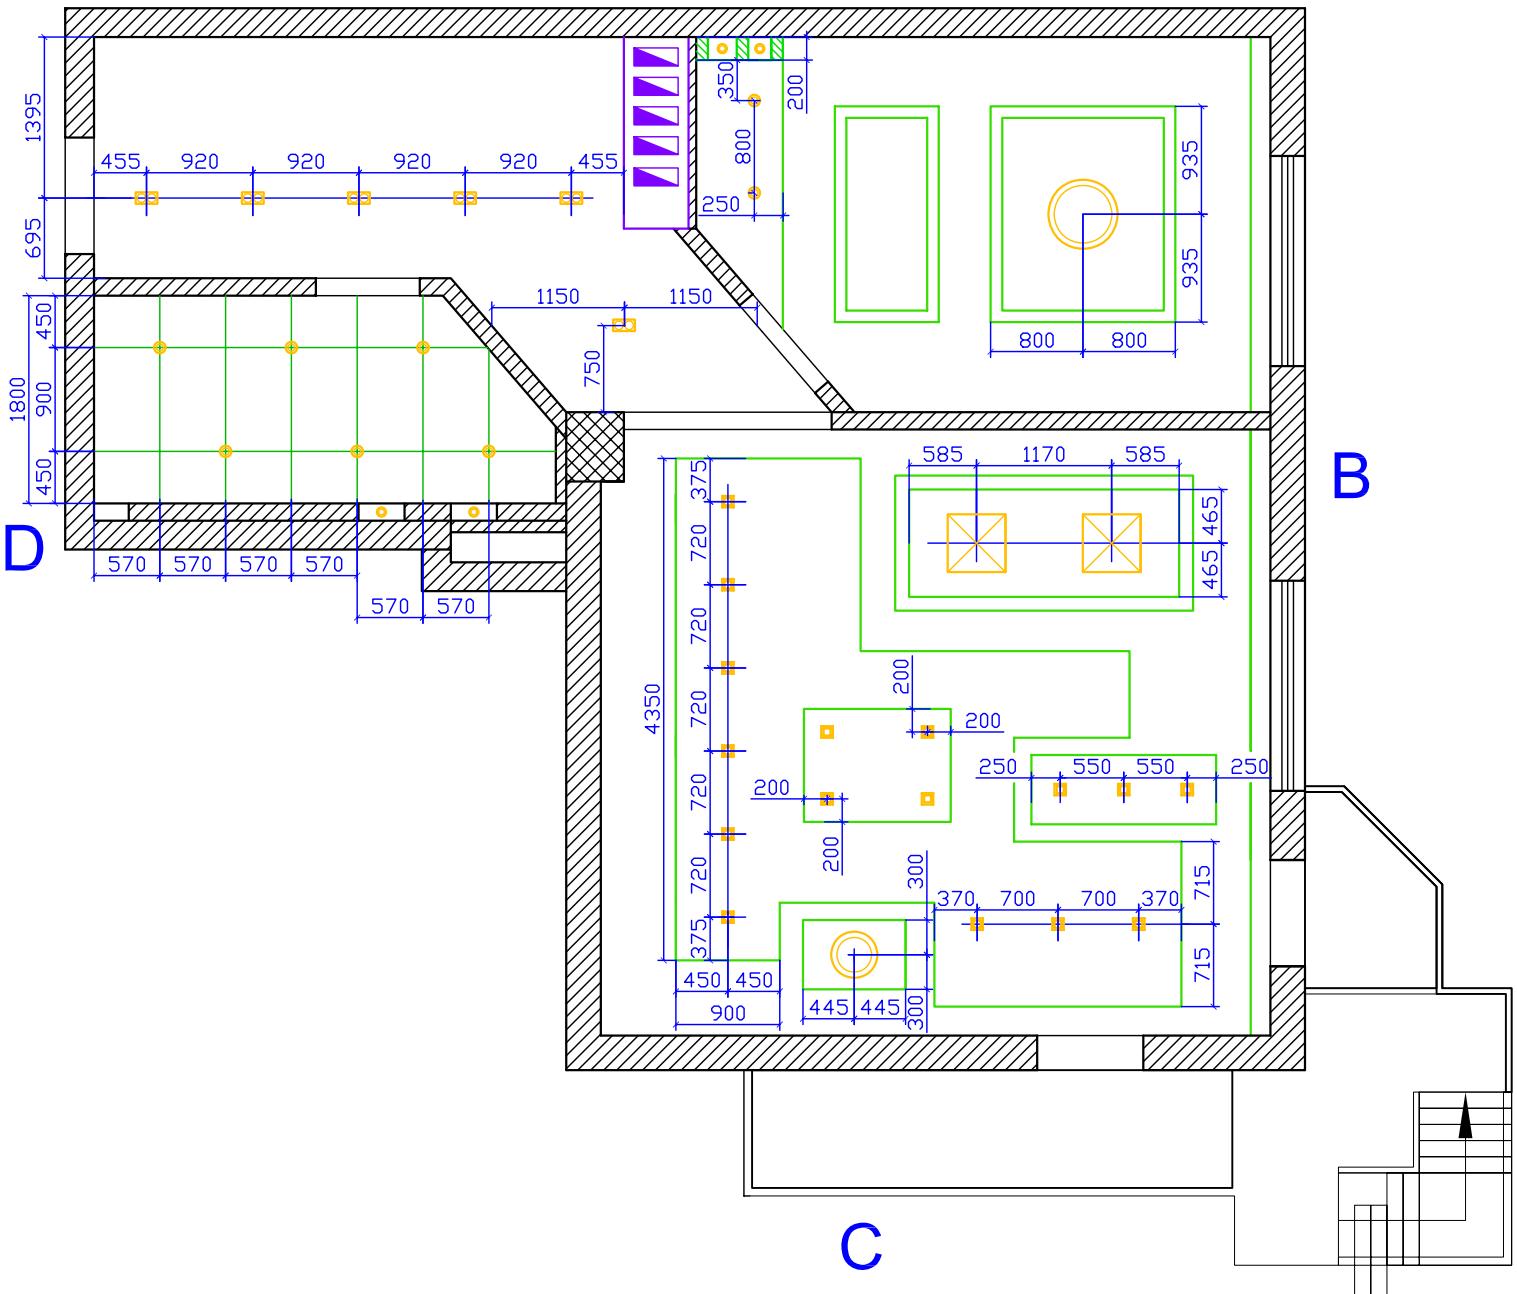


B

C

План расстановки розеток


A

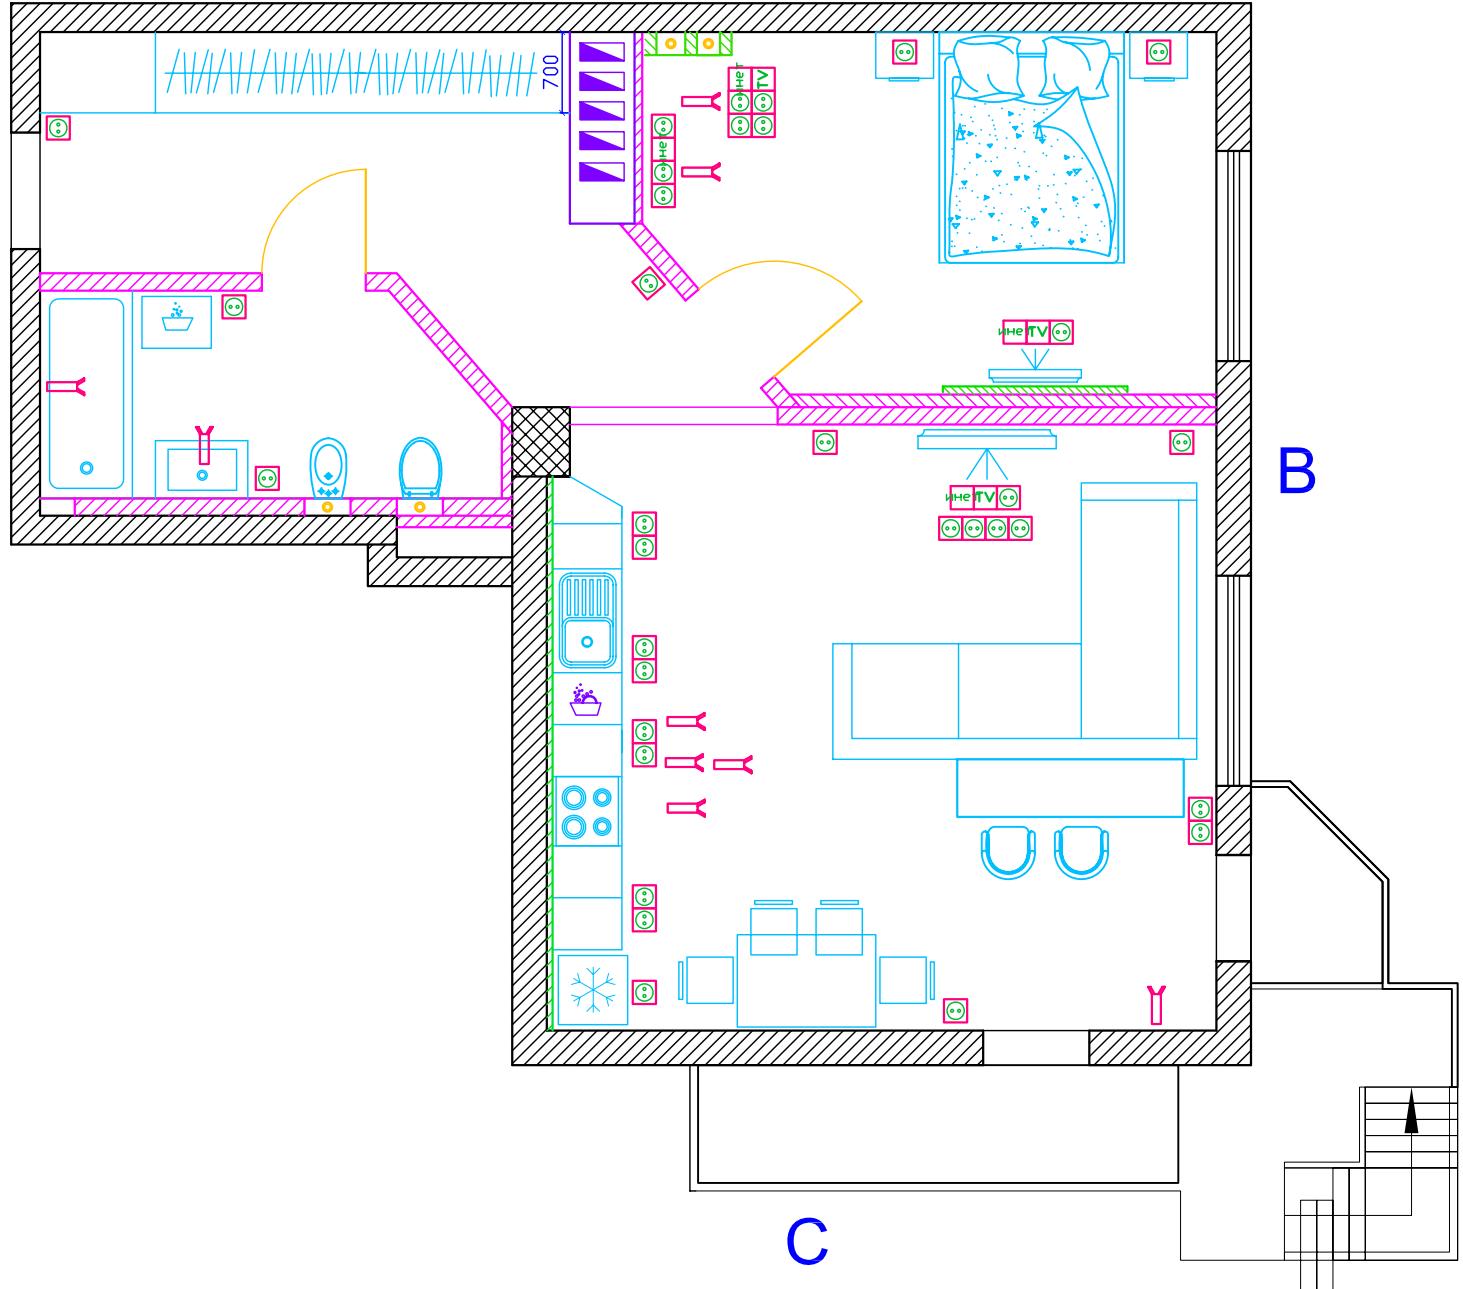


B

C

План включения светильников

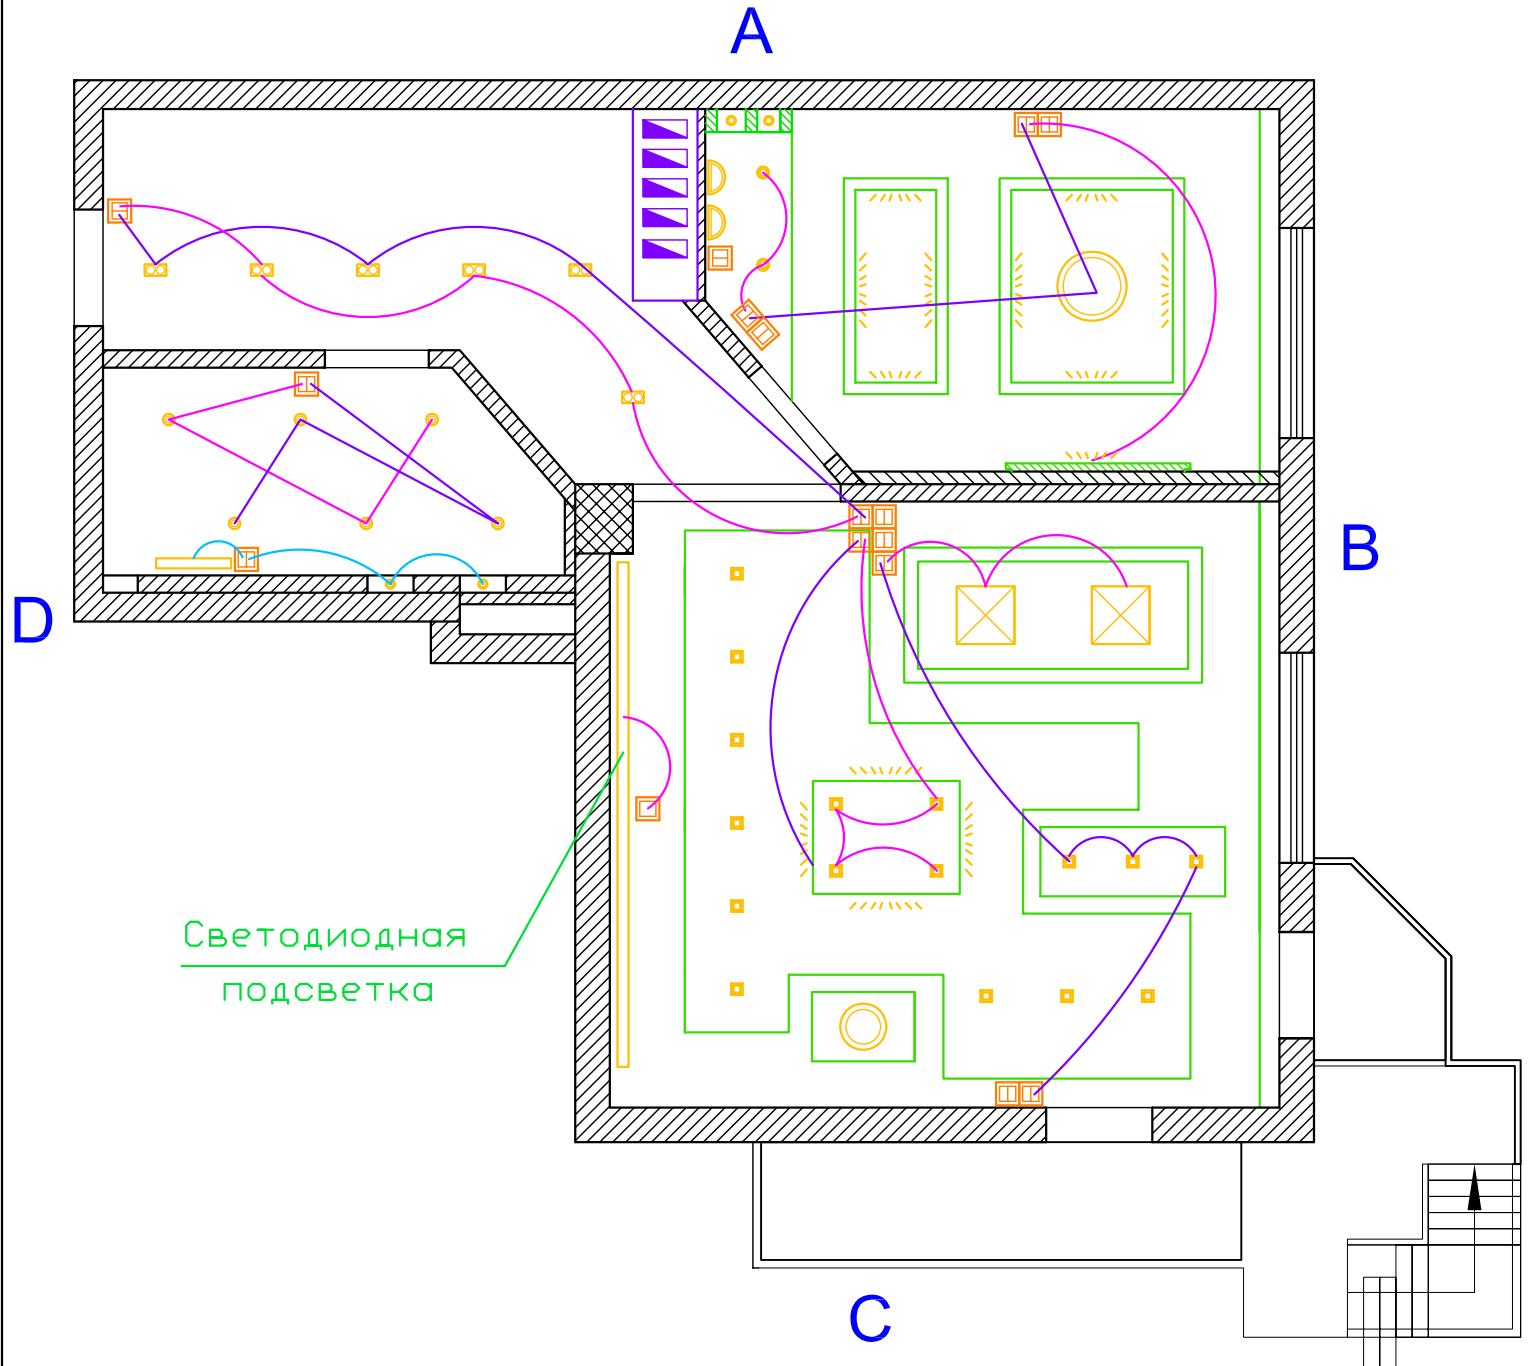


План включения светильников

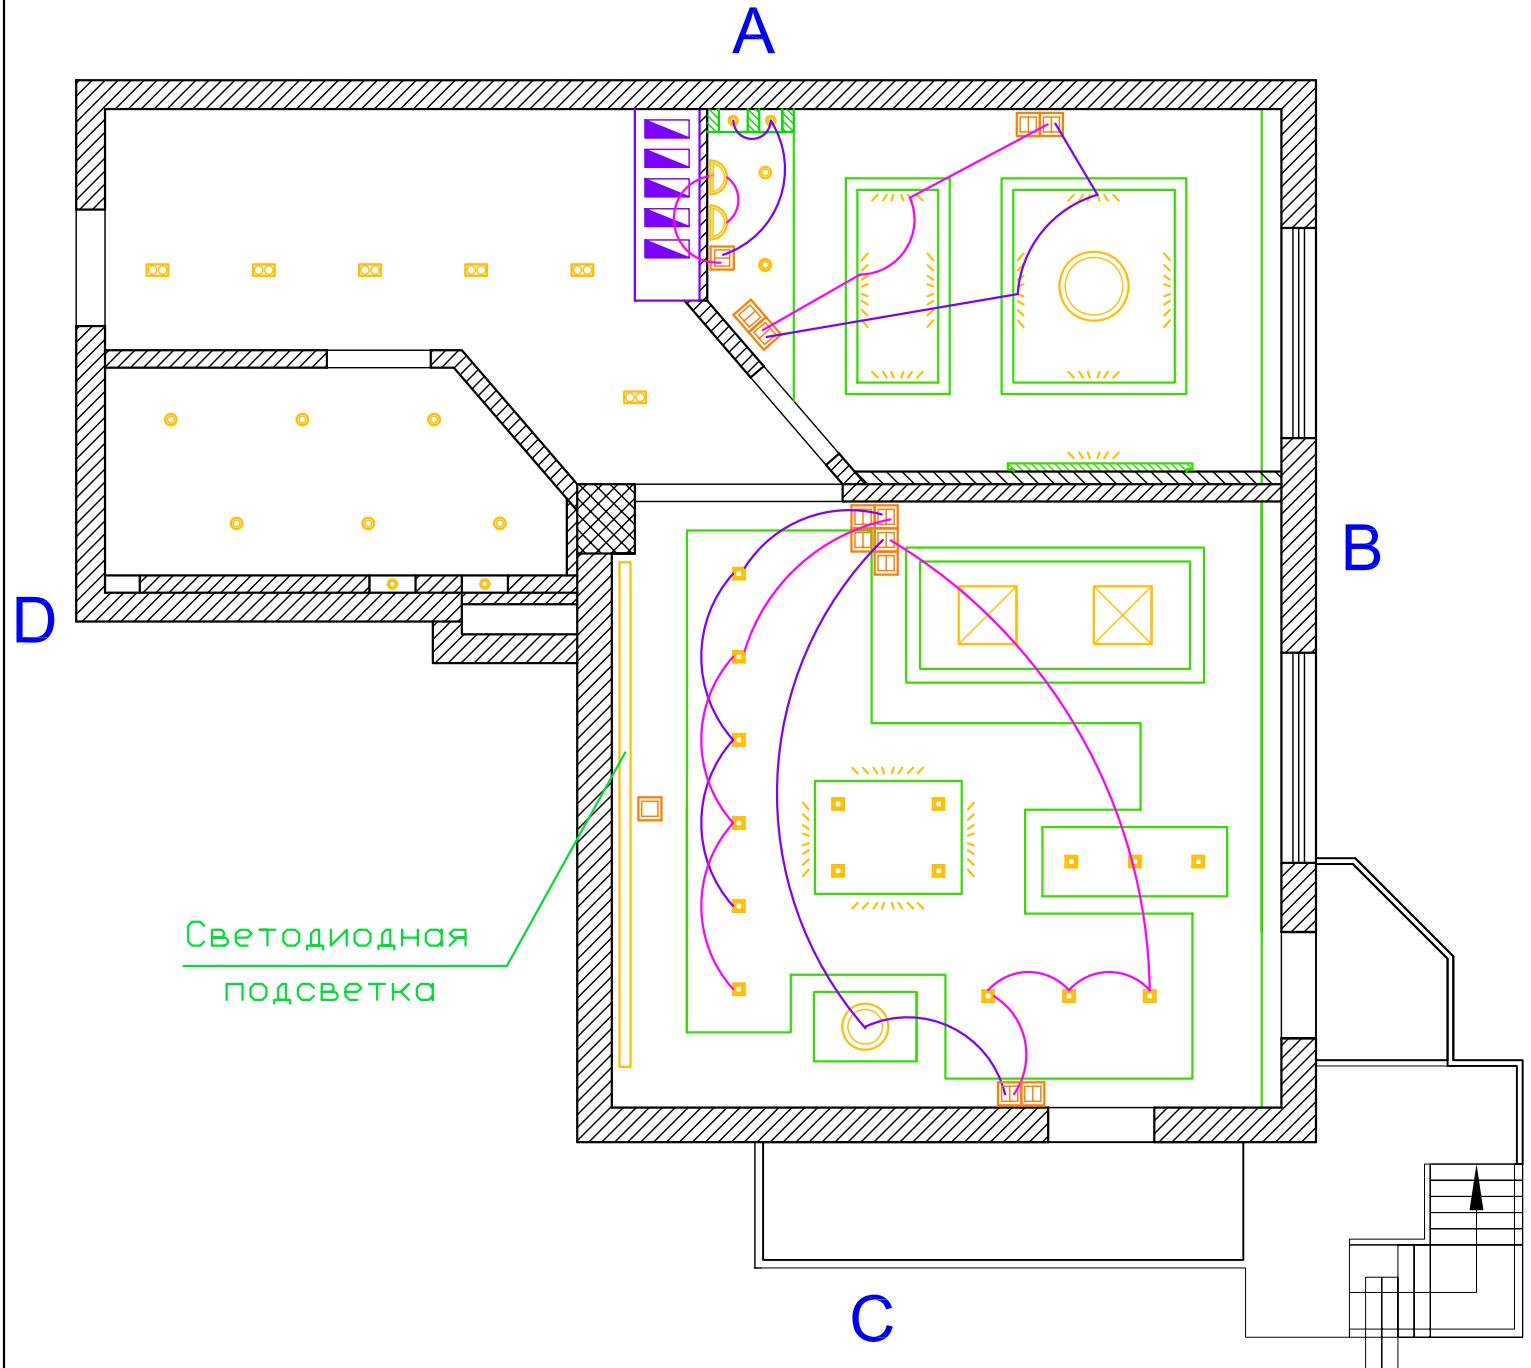




Развёртки стен кухни-гостиной

А

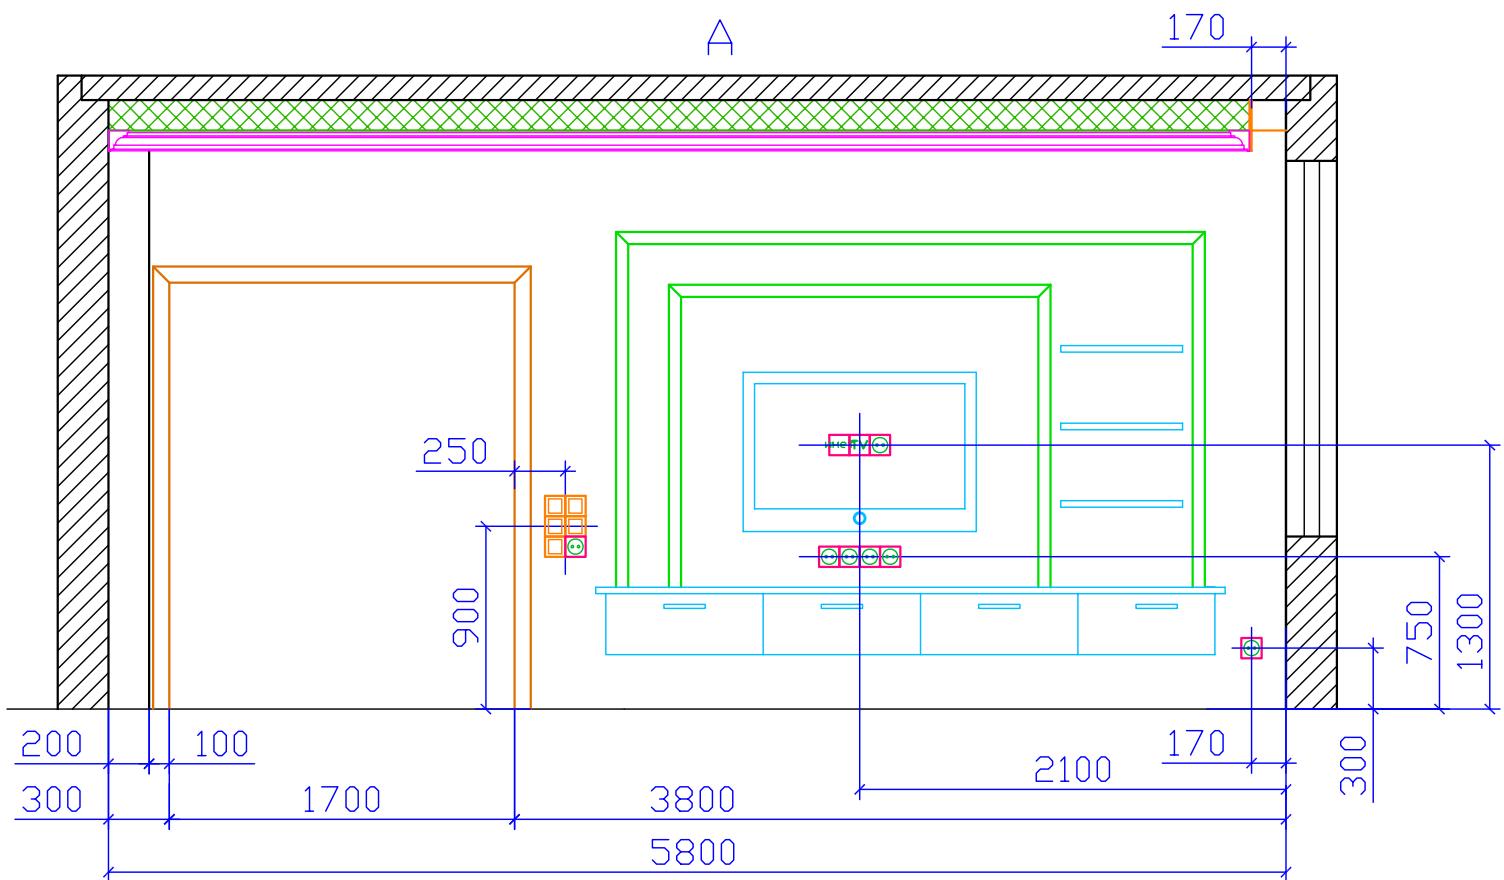

Развёртки стен кухни-гостиной


А

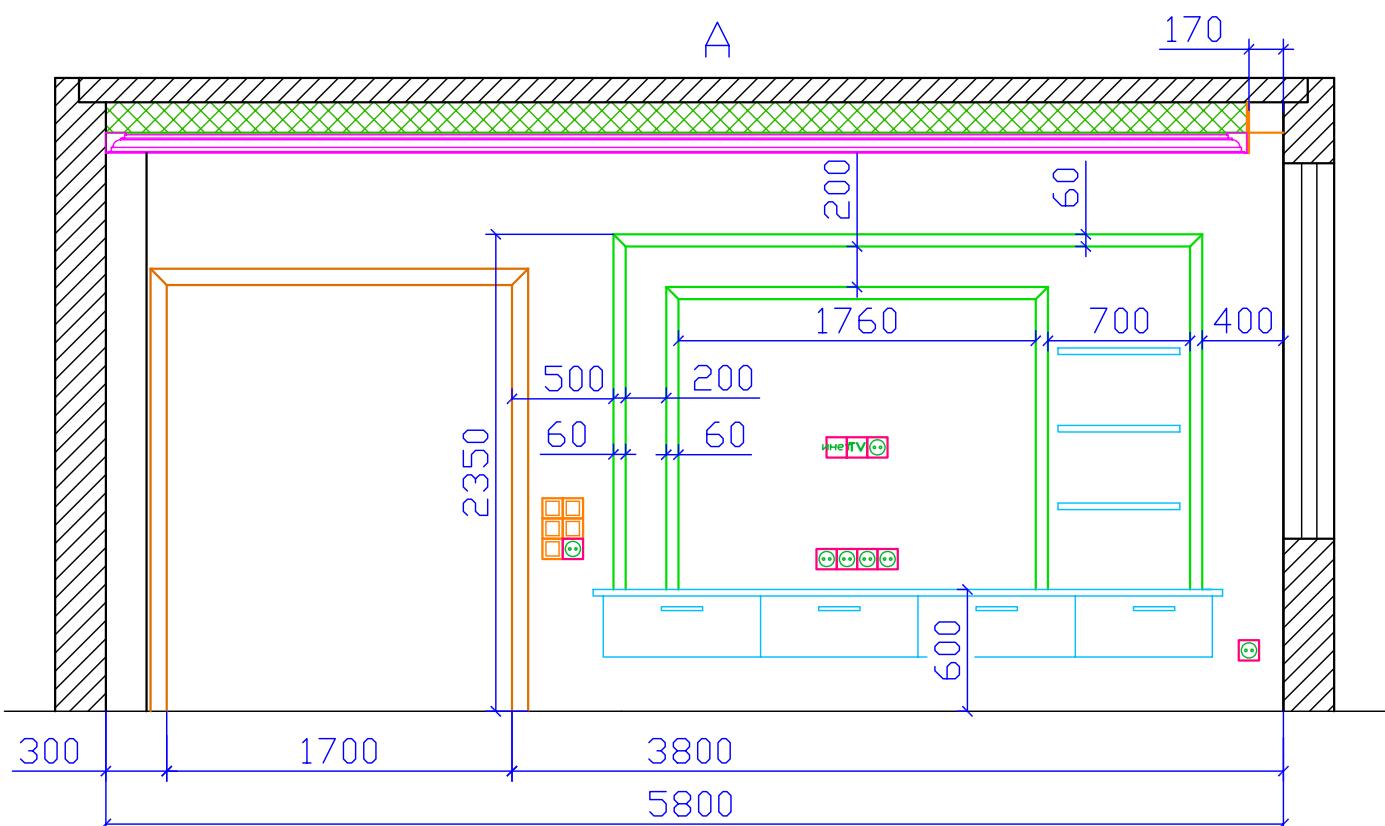

TRAFFIC MIX RECT – 30x60 =15шт

Развертки стен кухни-гостиной


B

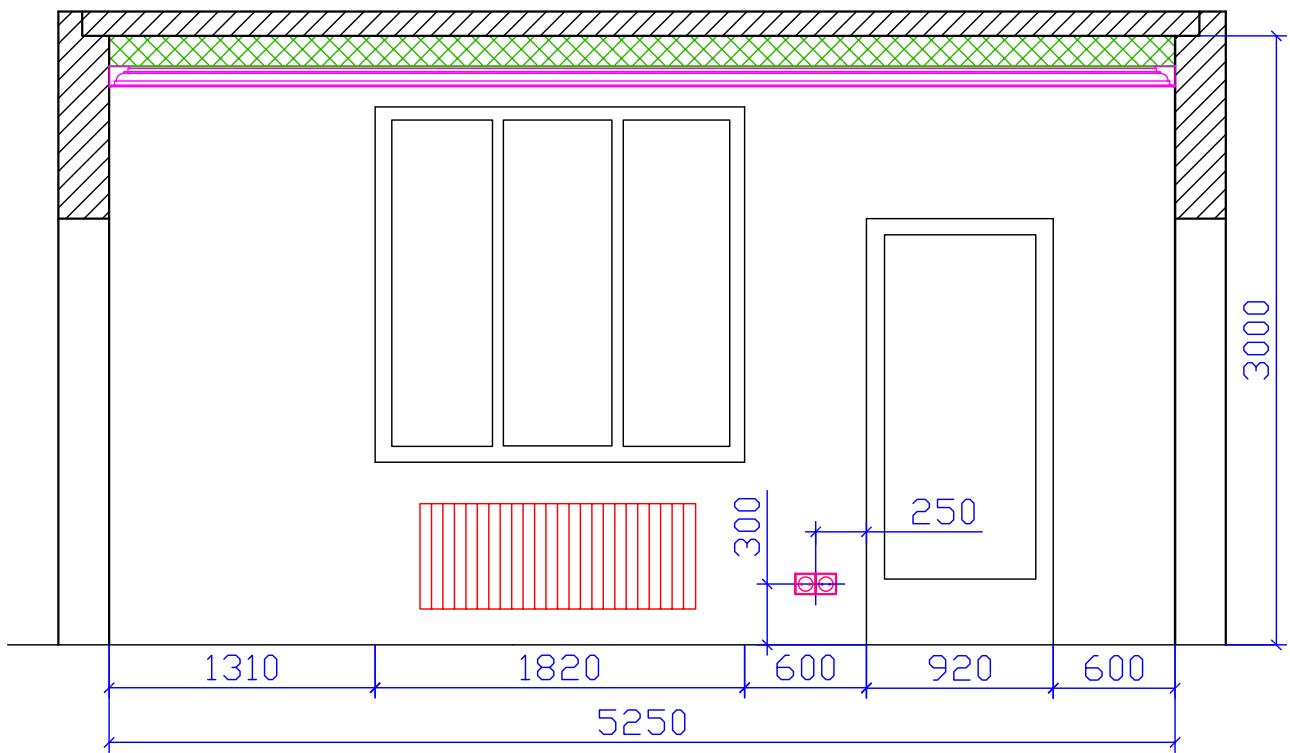

Развертки стен кухни-гостиной

C


КОРОБ В УРОВЕНЬ С КОЛОННОЙ

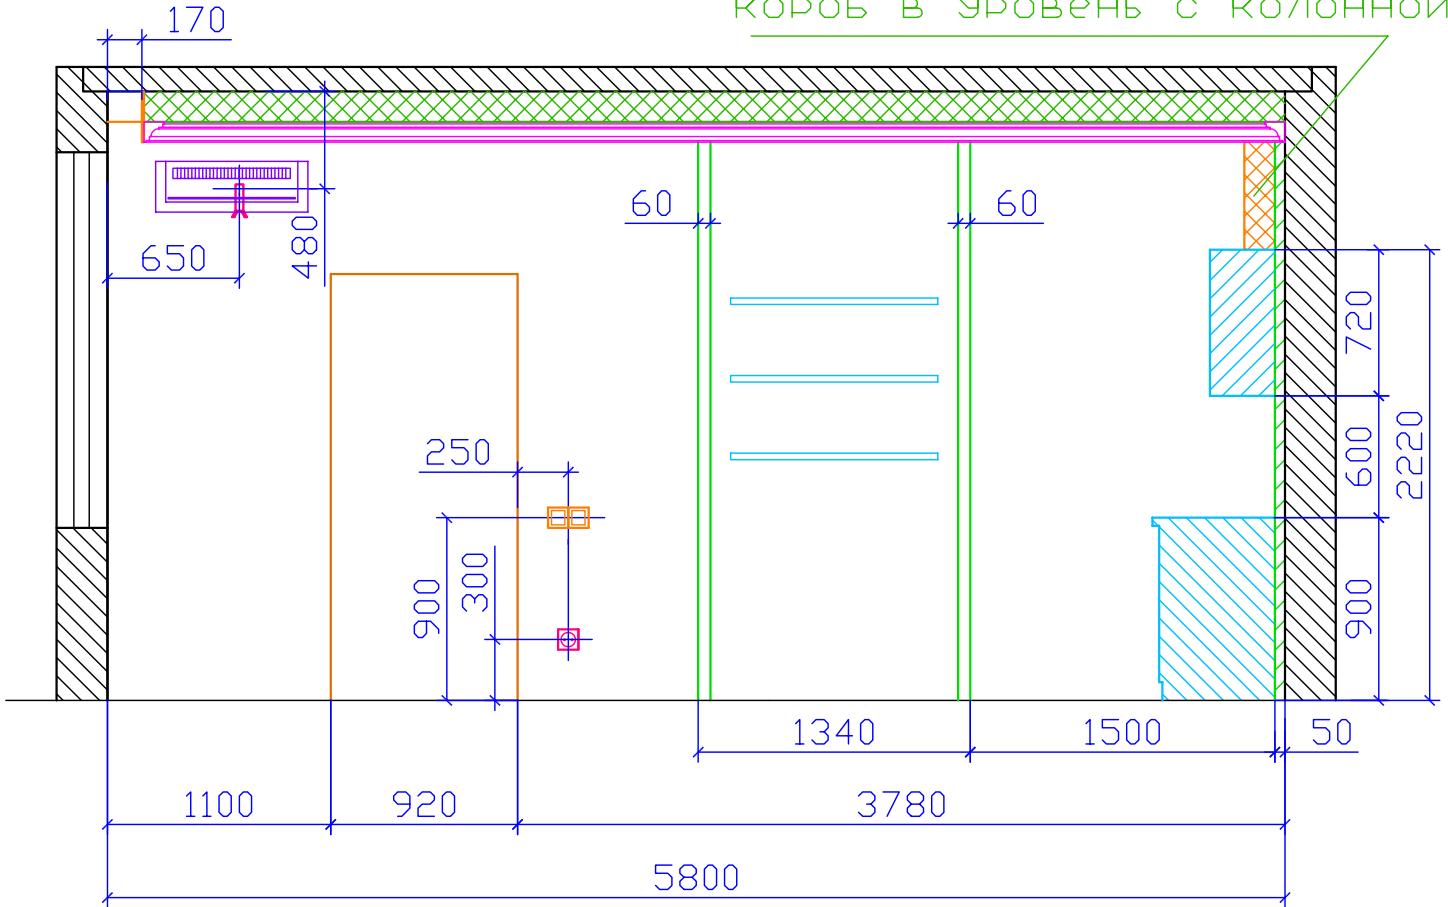

Развертки стен кухни-гостиной

D


КОРОБ В УРОВЕНЬ С КОЛОННОЙ

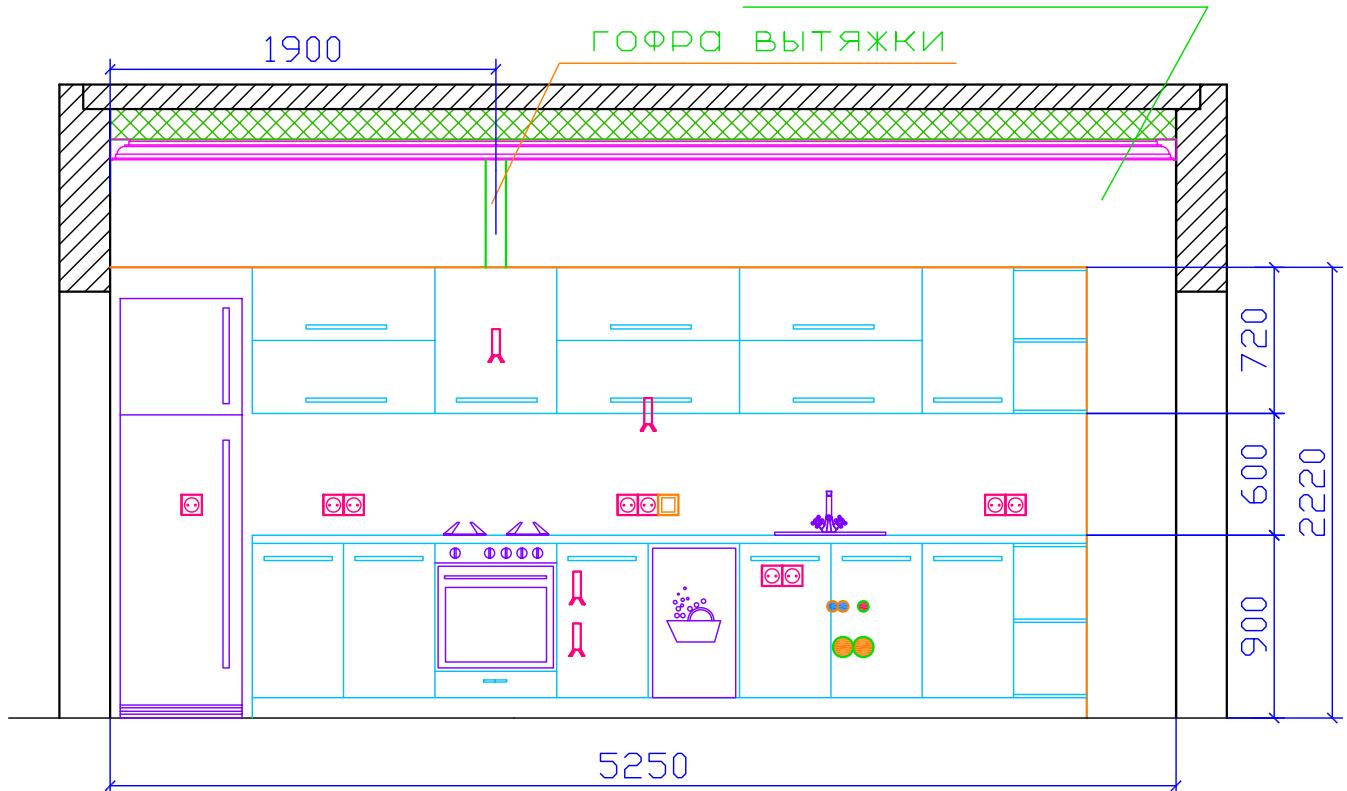

Развертки стен кухни-гостиной

D


Вытяжка

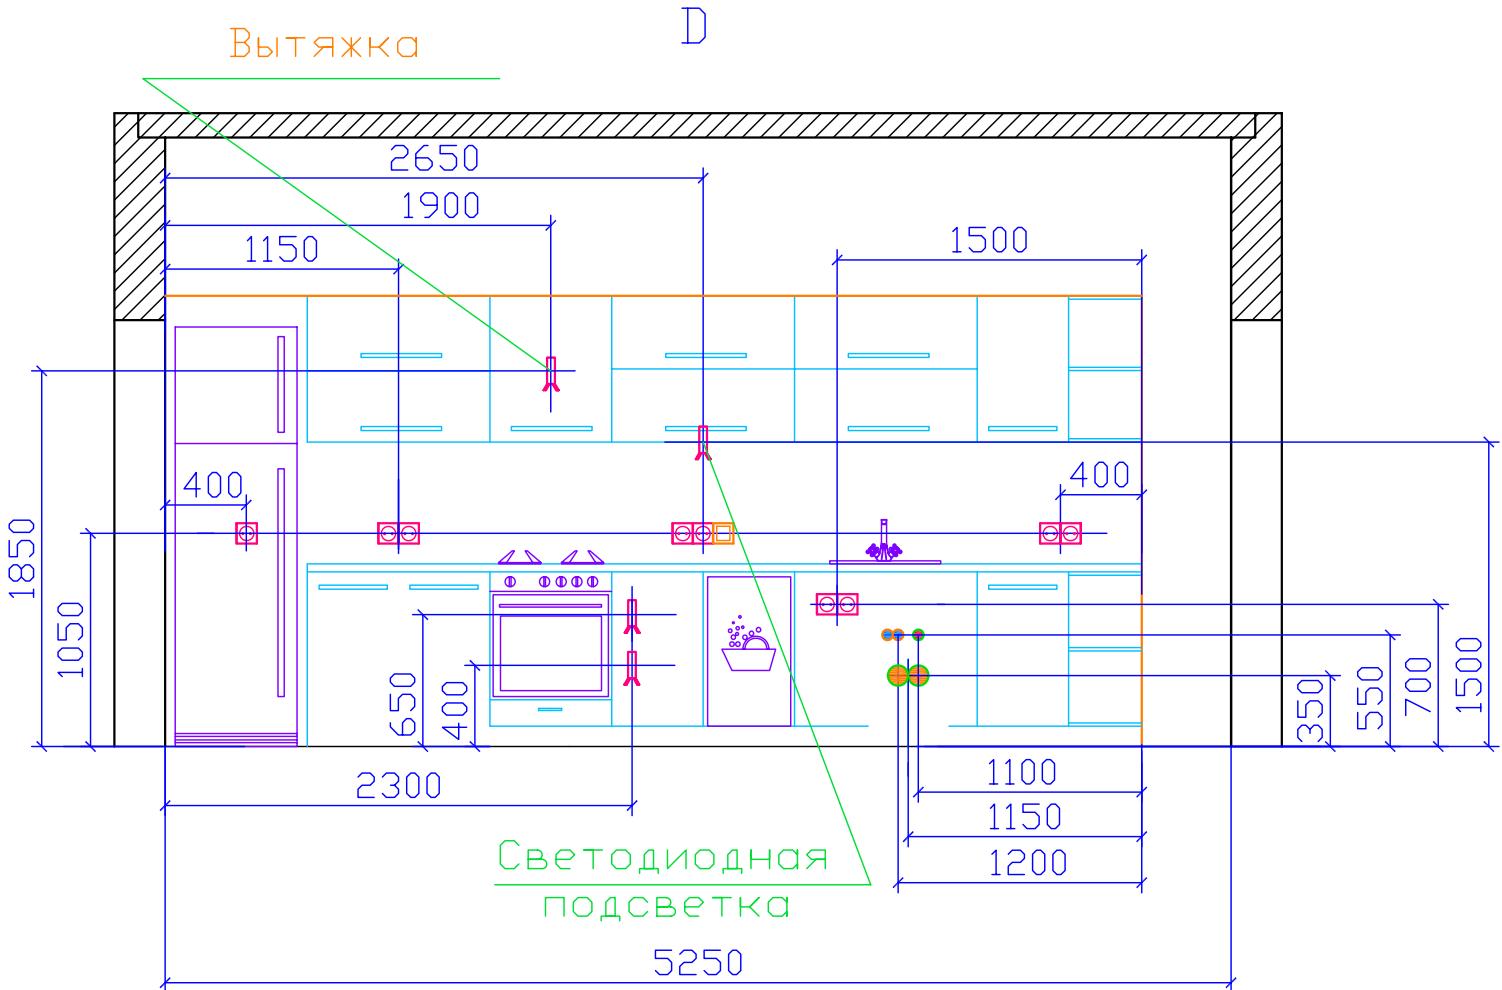




Развёртки стен коридора

D

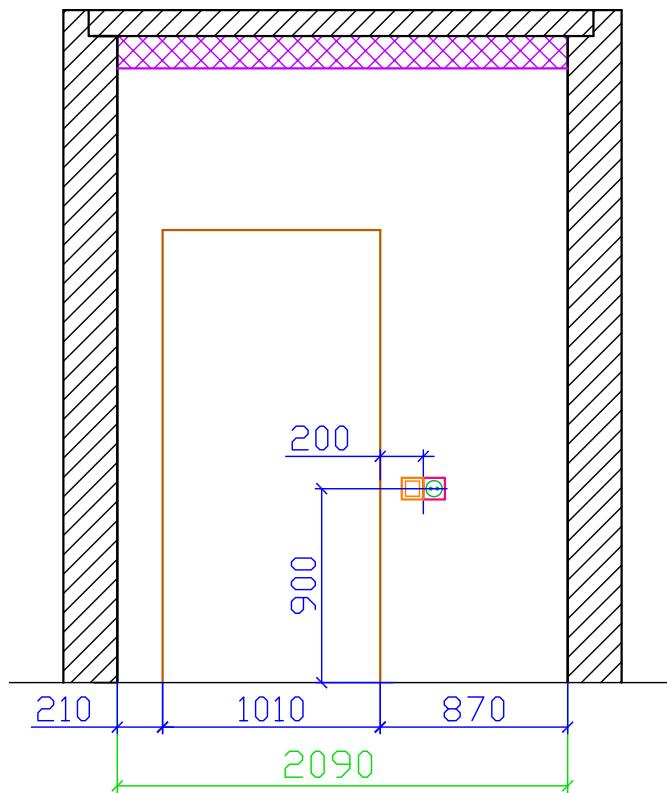

Развёртки стен коридора


A

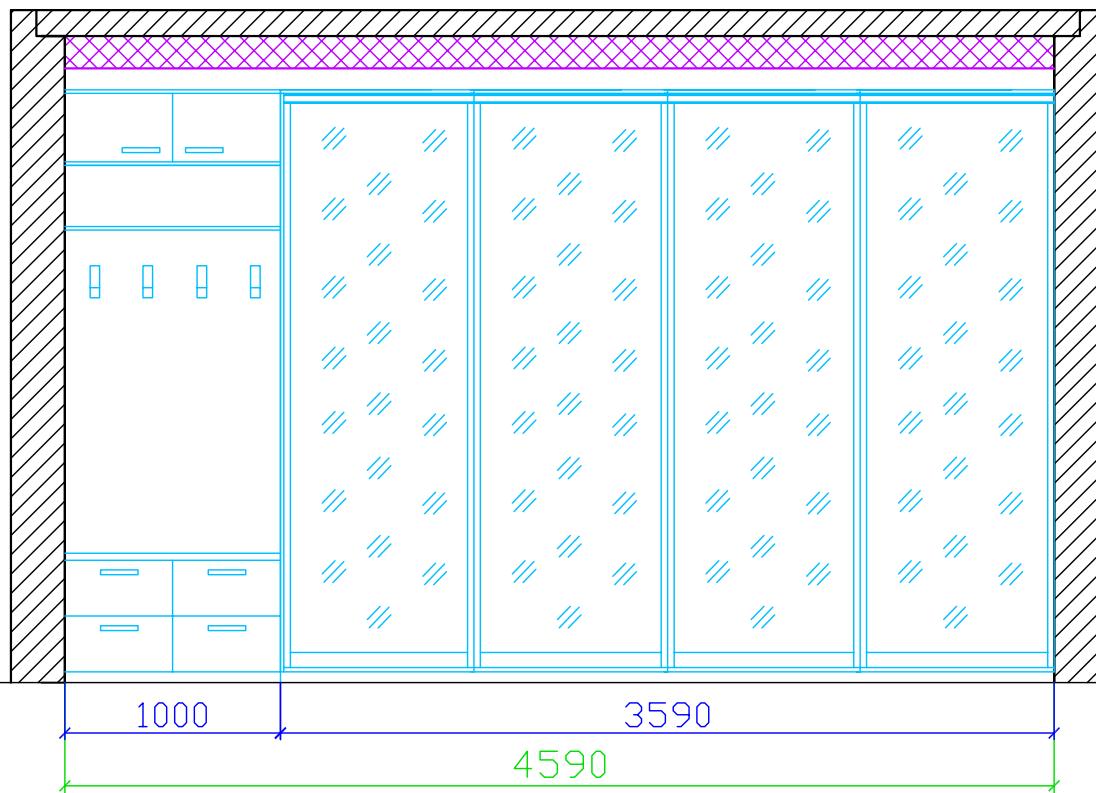

Развёртки стен коридора


лист

14

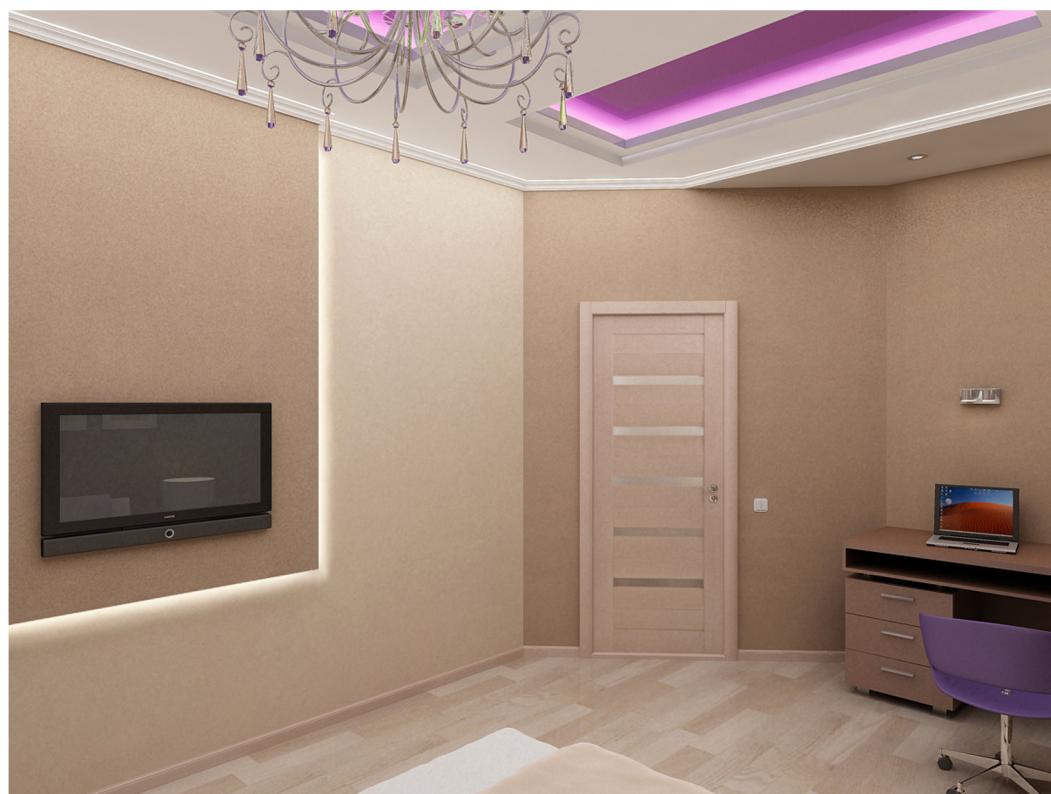


Развёртки стен спальни

А

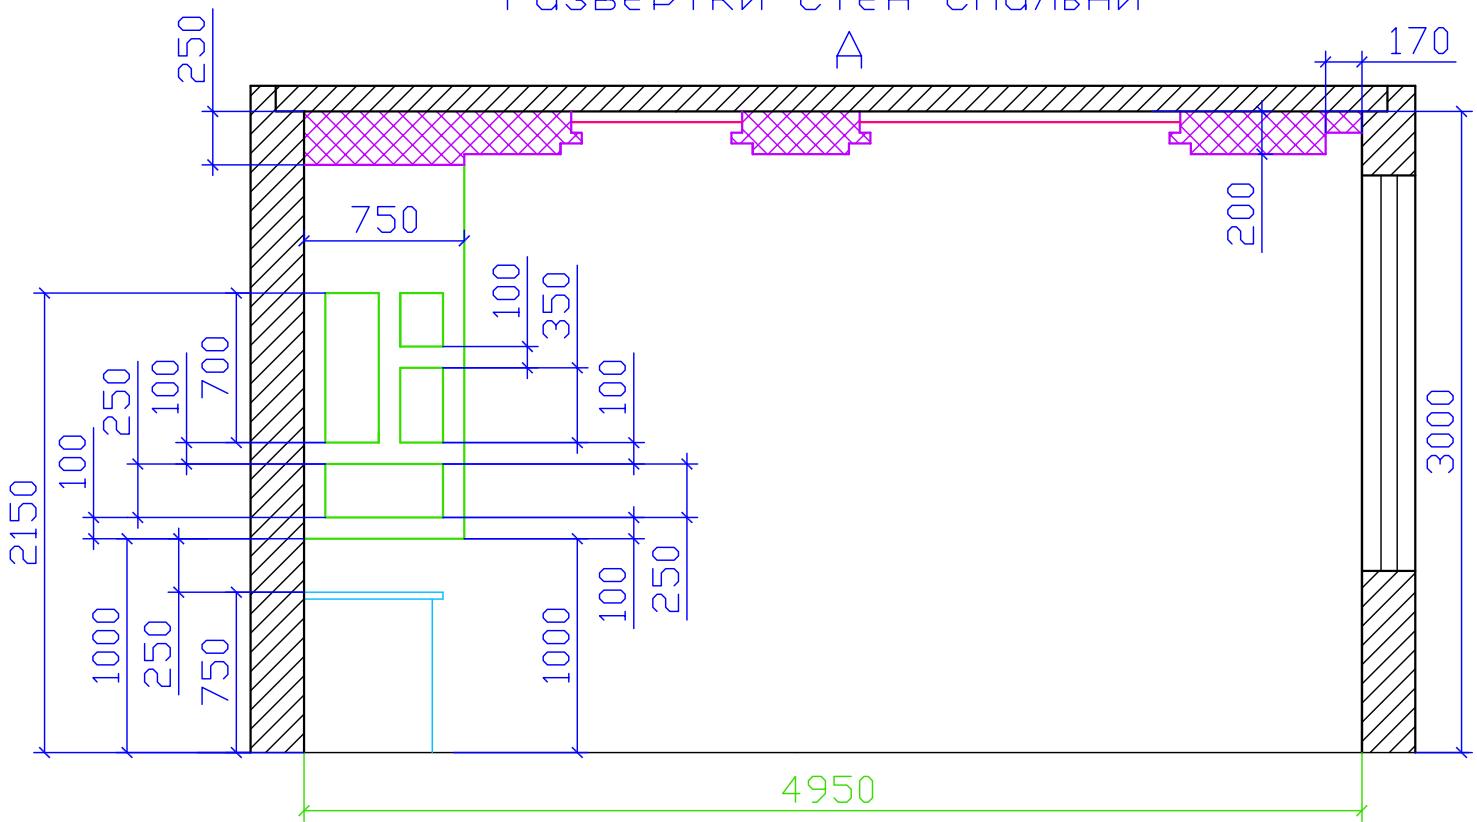


Развёртки стен спальни

А

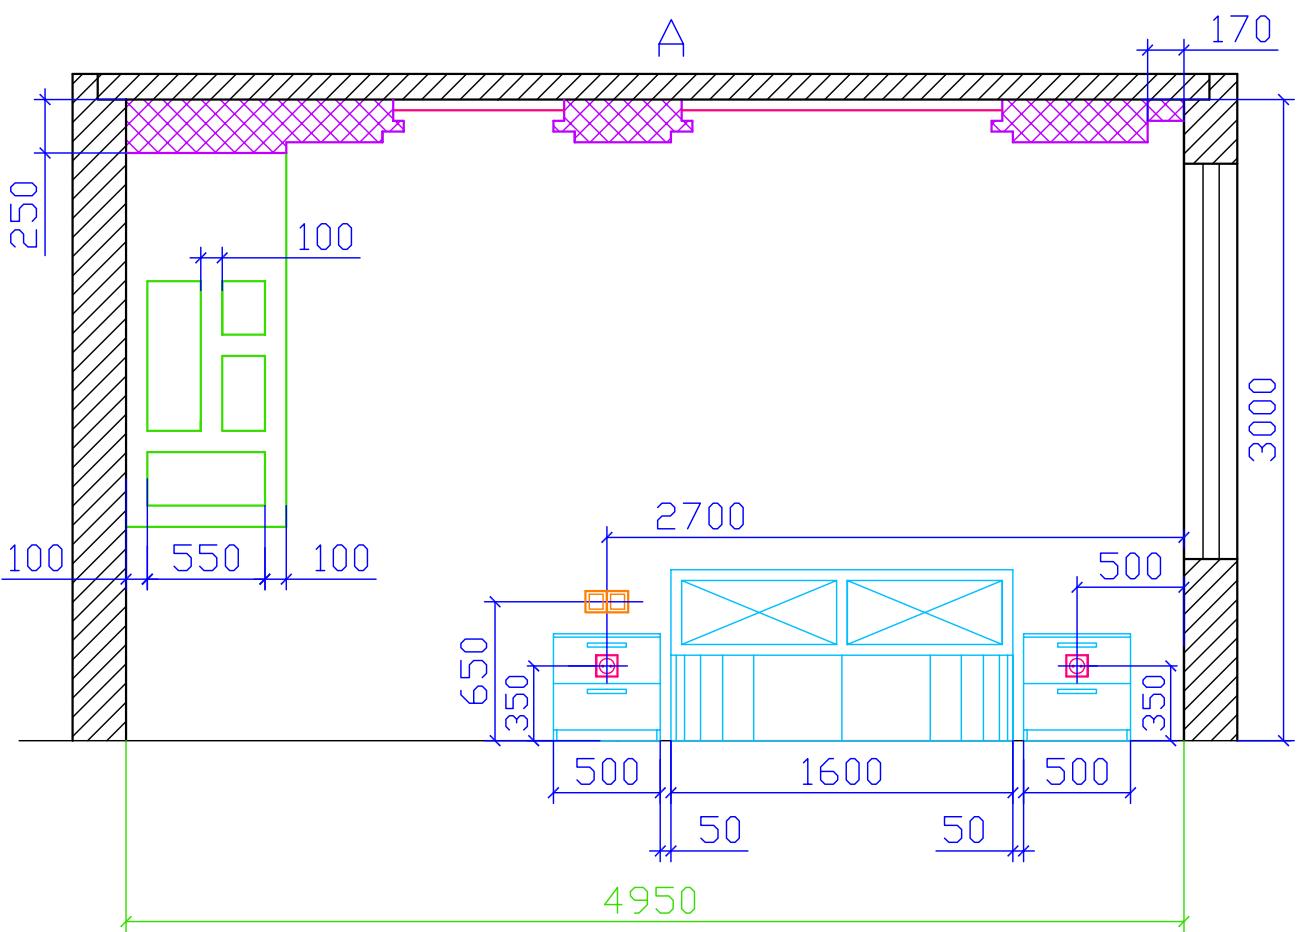



Развертки стен спальни

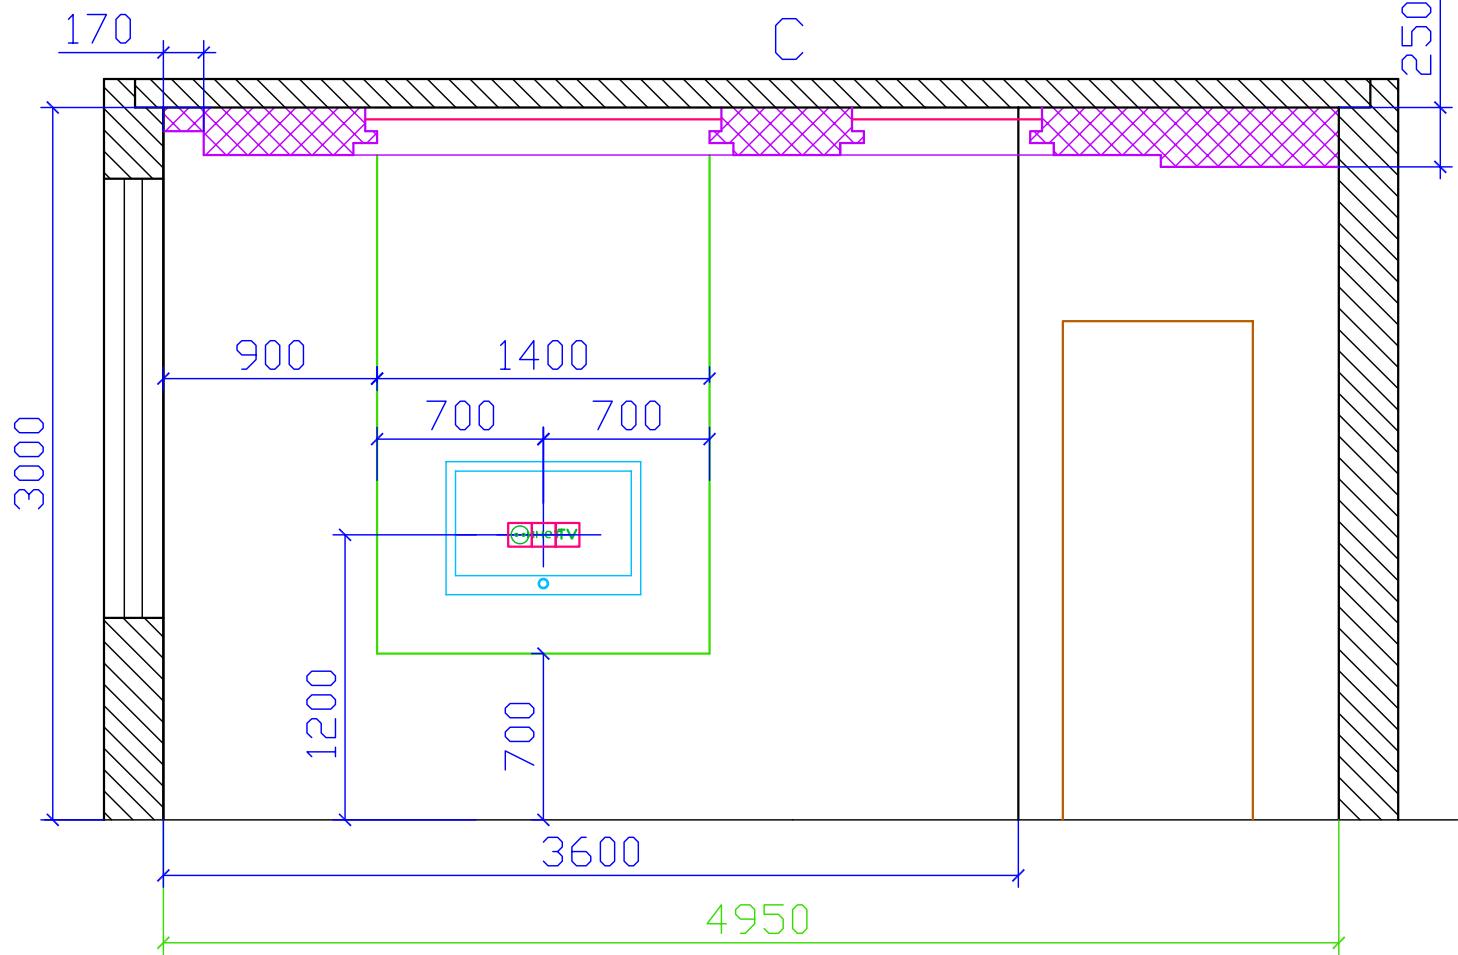

Развертки стен спальни


Д

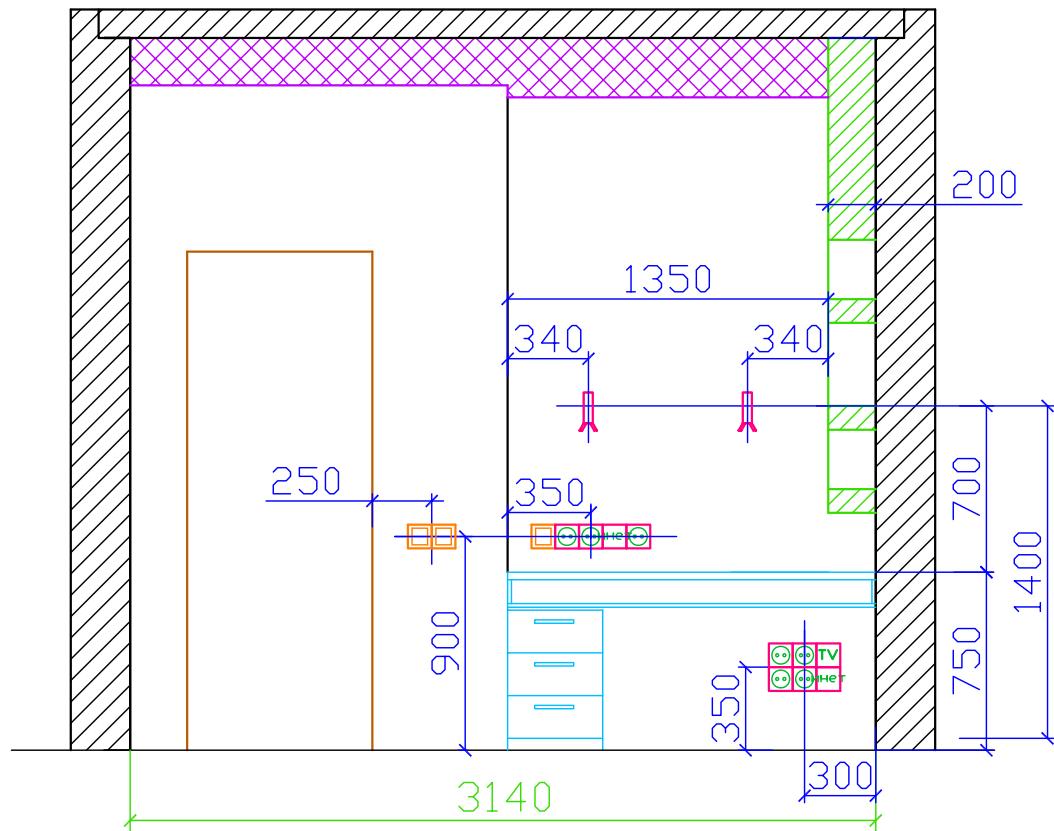

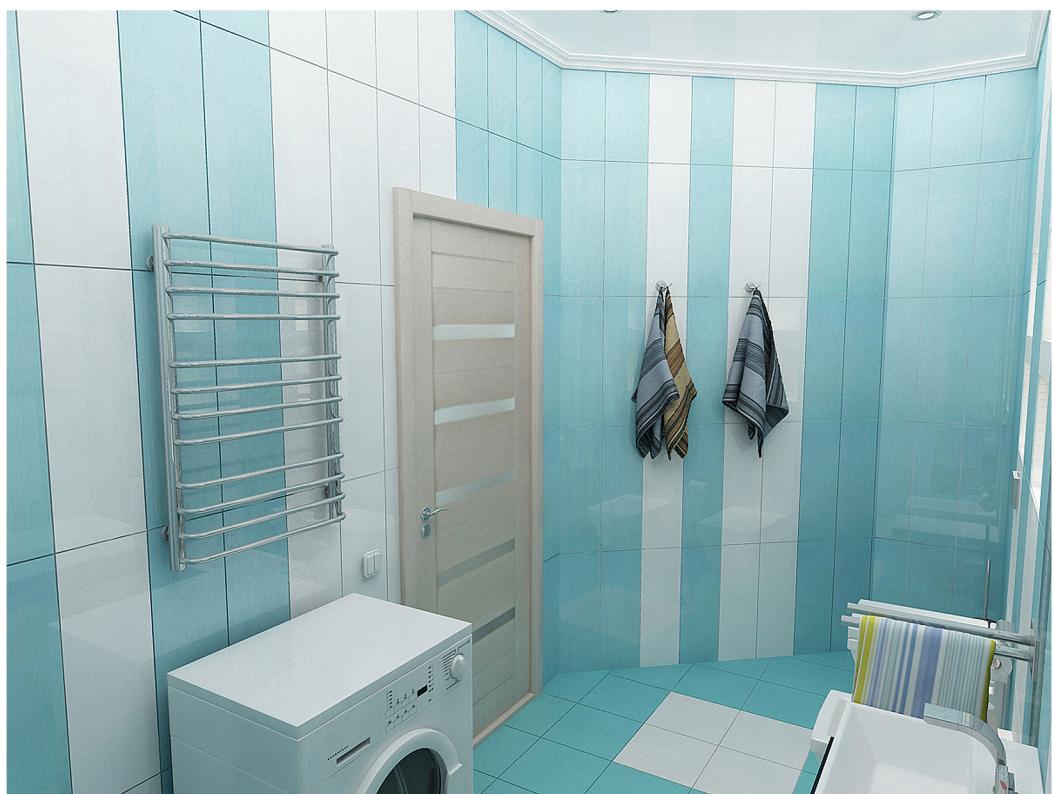


Развёртки стен ванной

А

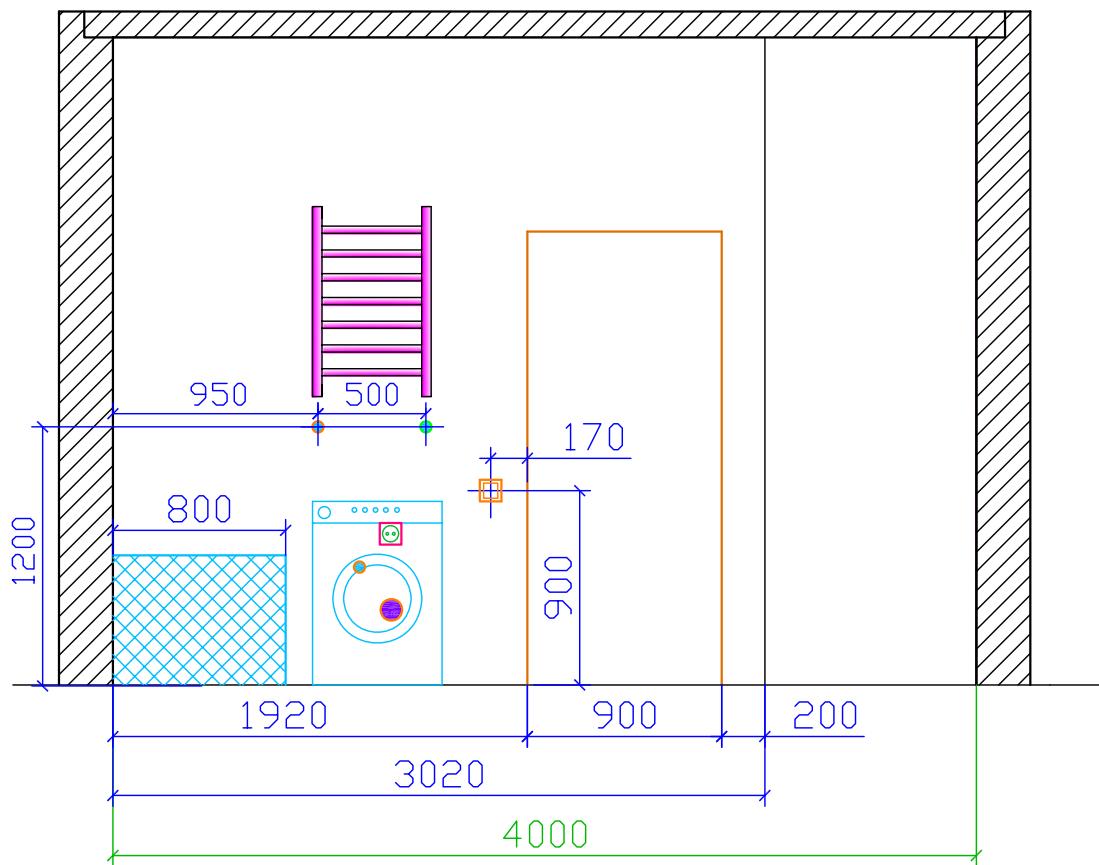


Развёртки стен ванной

А

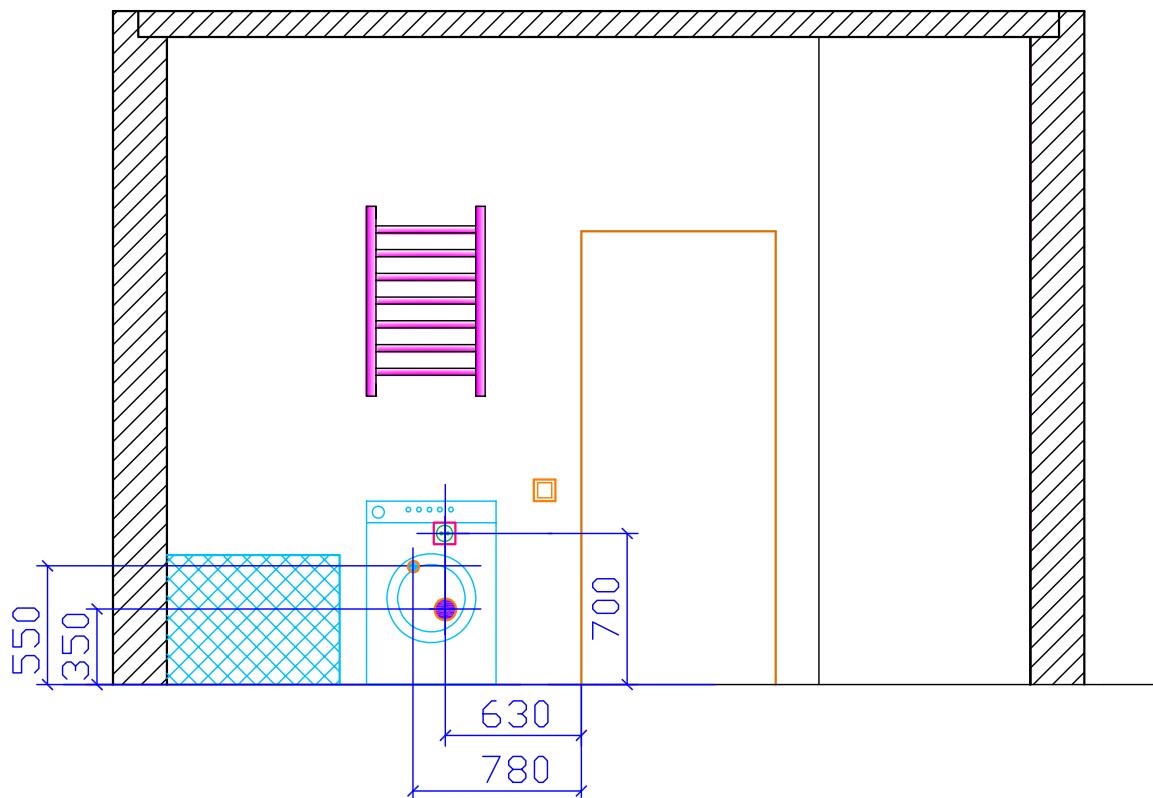


Развёртки стен ванной



A

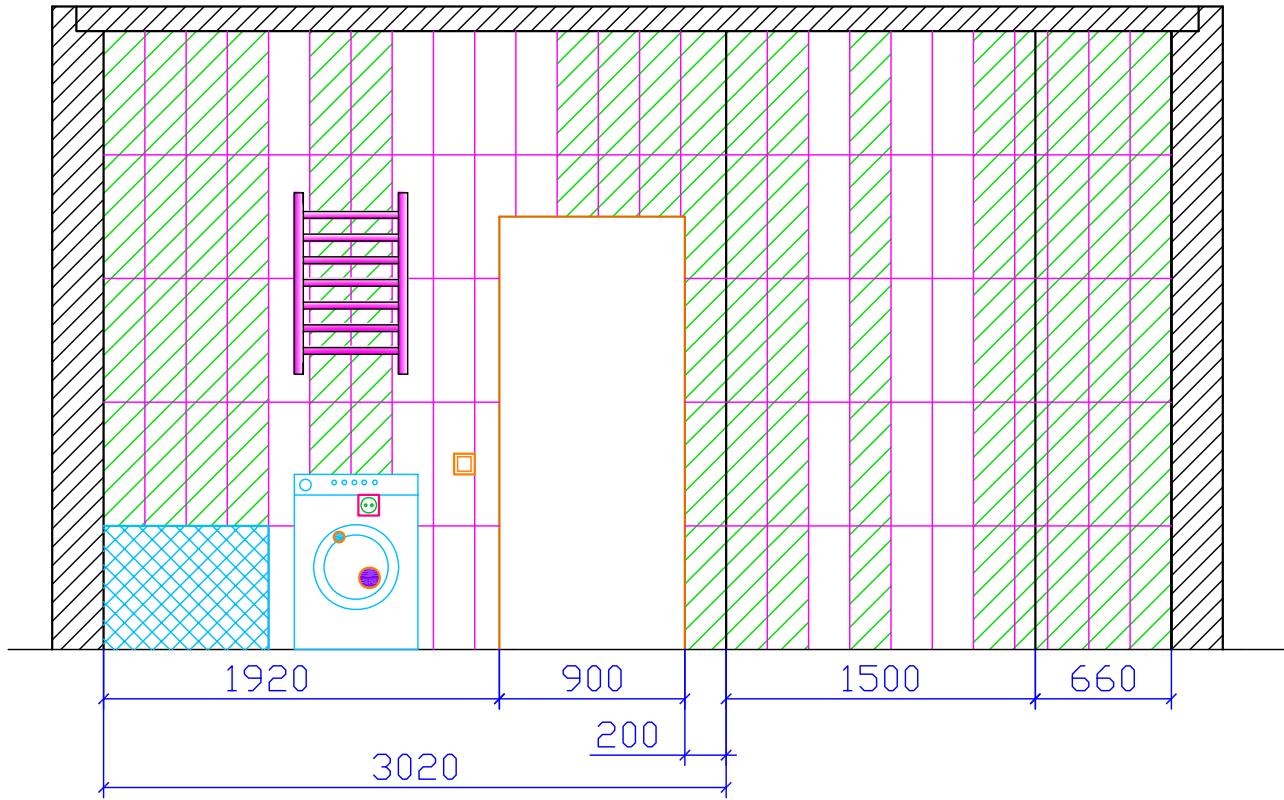


Развёртки стен ванной

D

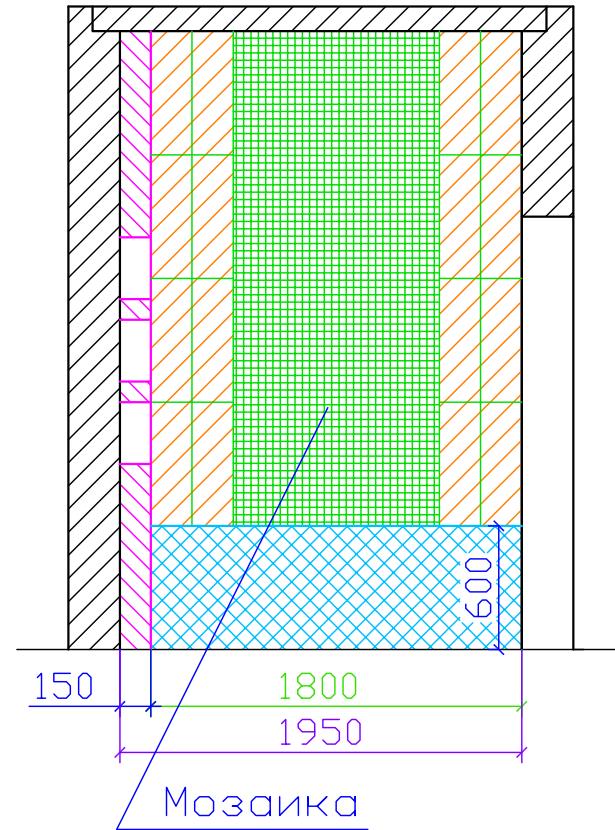

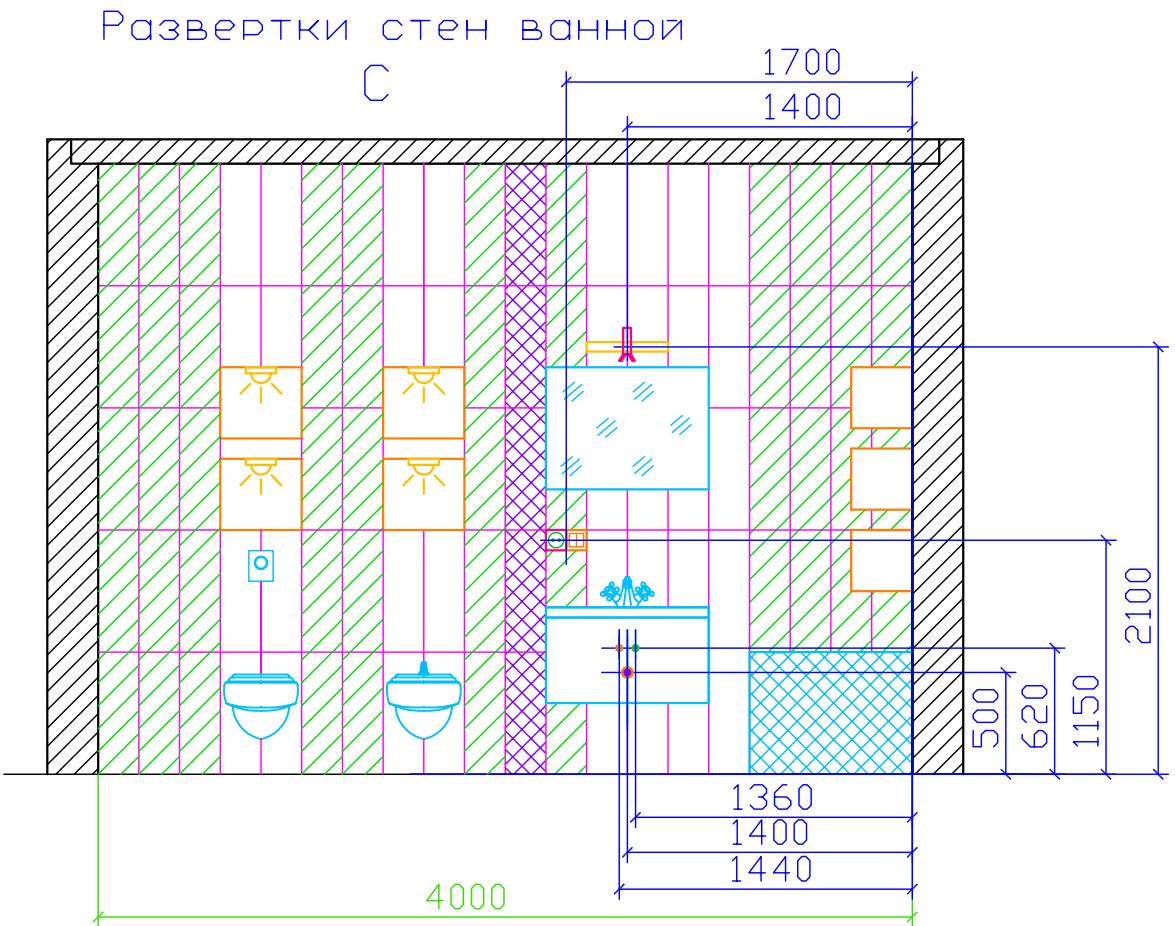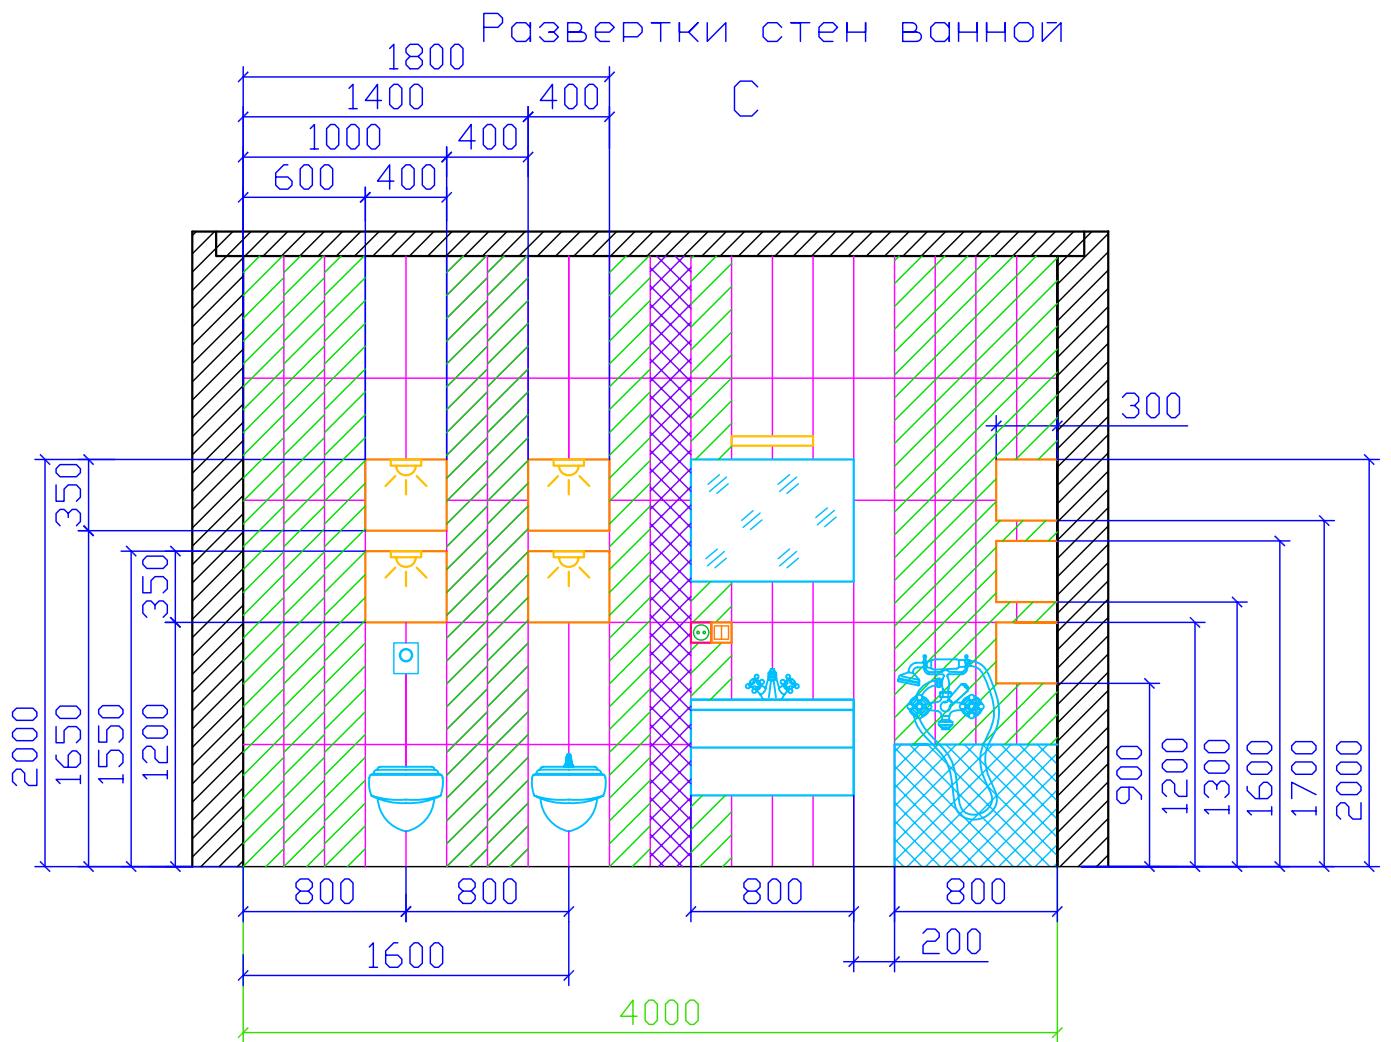

Развертки стен ванной

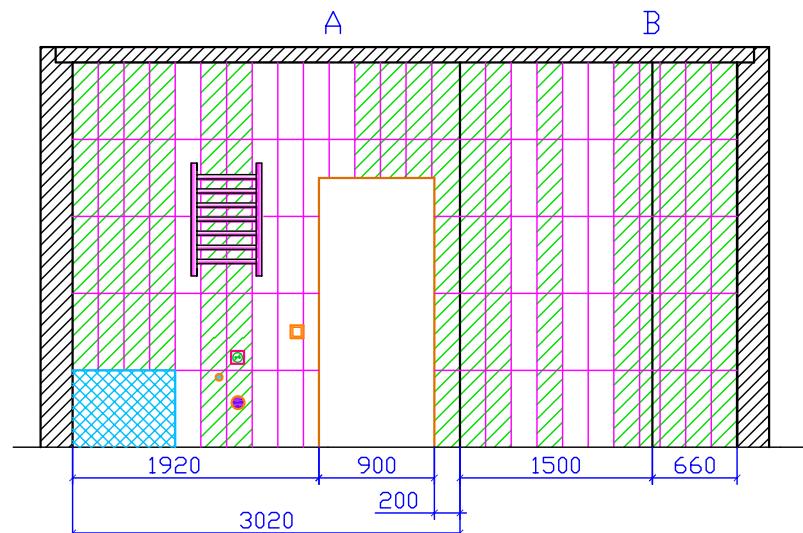

- Синяя -41шт


- Синяя -40шт

- Белая -22шт

- Белая -15шт

Развертки стен ванной

C

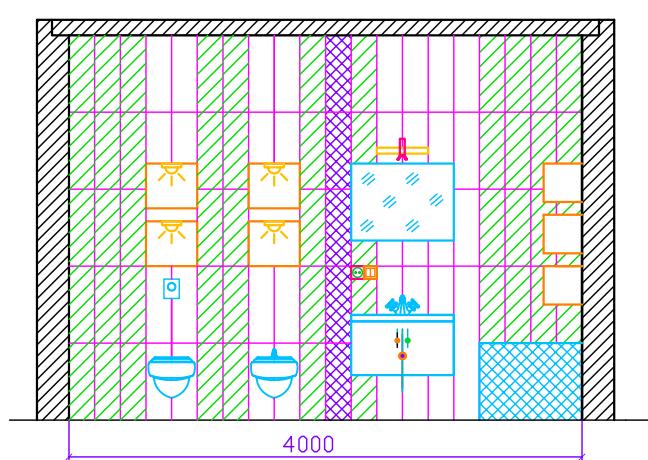

- Синяя -55шт

- Синяя -20шт

- Белая -38шт


- Мозаика -3м²

- Декор -5шт

- Мозаика -2.5м²

Развертки стен ванной

D

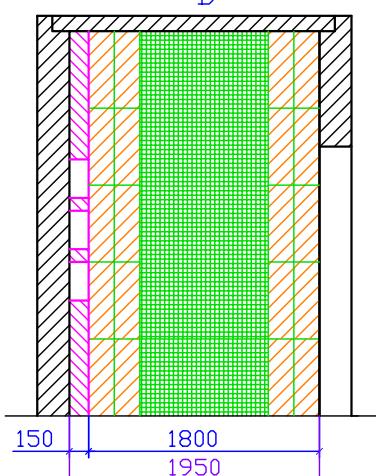

- Синяя -20шт

- Мозаика -3м²

Общее кол-во плитки без запаса

- Синяя -55+20+41+40=156шт

- Синяя -67шт

- Белая -38+22+15=75шт

- Белая -8шт

- Декор -5шт

- Мозаика -5.5м²

Общее кол-во плитки ванной

Лист

20